-ESTACIÓN TOLOSA-

km 50,555

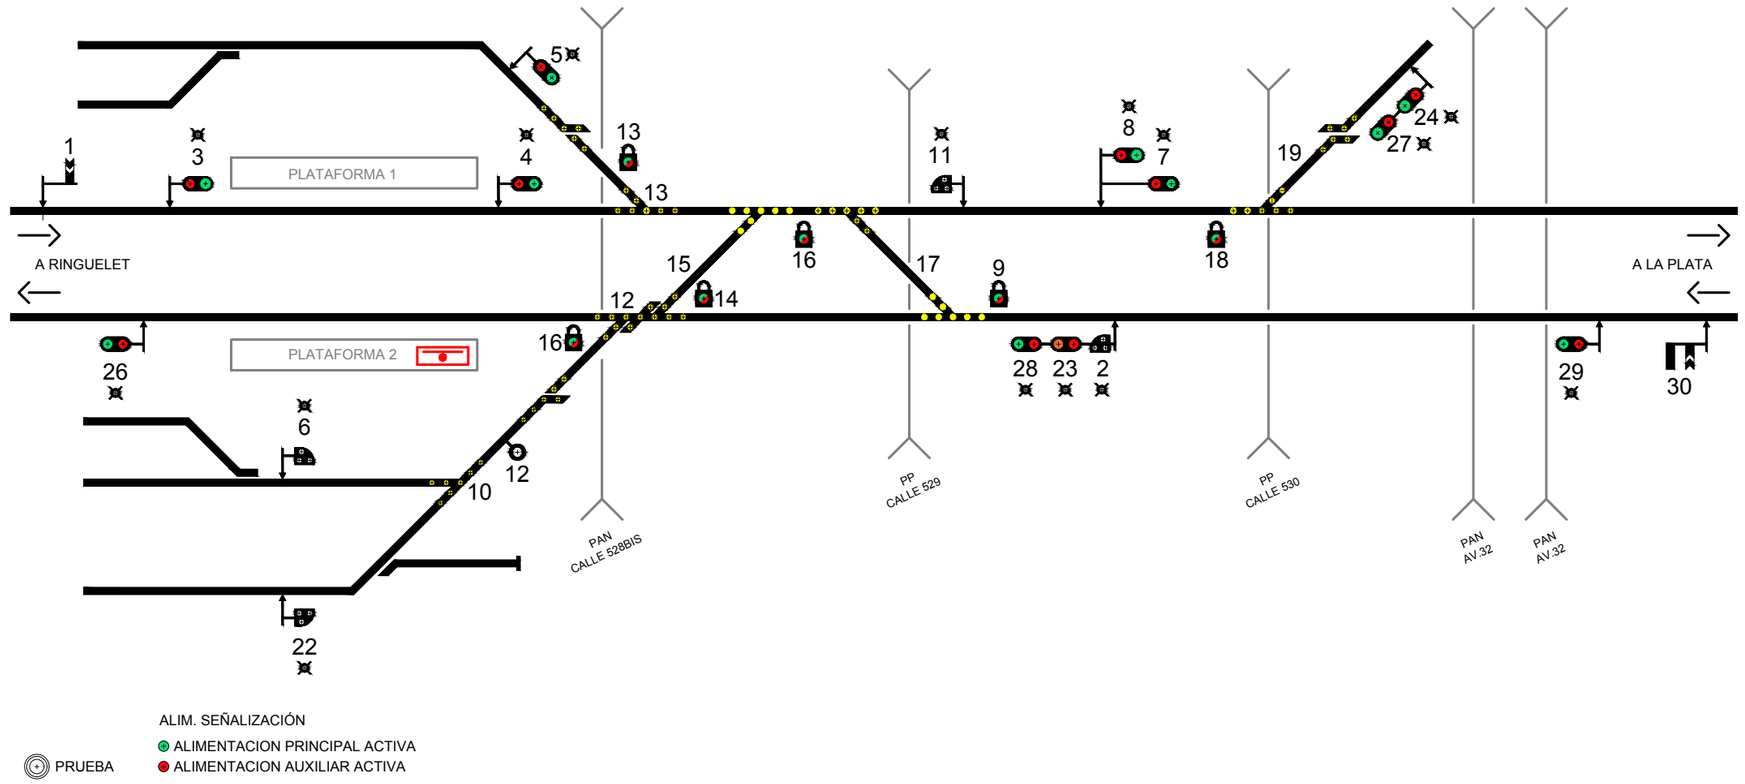

500

900

TIPO DE LED	SEÑALES	CANT.
Led Blanco	IM2(4), SS3(1), SS4(1), SS5(1), IM6(4), SS7(1), SS8(1), IM11(4), IM22(4), SM23(1), SS24(1), SS27(1), SS28(1), SS29 (1)	26
Led Verde	SS3(1), SS4(1), SS5(1), SS7(1), SS8(1), SS24(1), SS27(1), SS28(1), SS29 (1)	9
Led Naranja	SM23(1)	1
Led Rojo	SS3(1), SS4(1), SS5(1), SS7(1), SS8(1), SM23 (1) SS24(1), SS27(1), SS28(1), SS29 (1)	10
Led Amarillo	CA10(7), CA12(14), CA13(13), CA15(12), CA17(14), CA19(13)	73
Led Bicolor (V/R)	CJ9(1), CJ13 (1), CJ14 (1), CJ16 (1), CJ18(1)	5

REV	DESCRIPCIÓN	FECHA	PROYECTÓ	EJECUTÓ	REVISÓ	APROBÓ
1	Modificación de semáforos señales 28, 23, 2	26/07/18	FNAV	FNAV	GVILL	
0	PRELIMINAR PARA EVALUACIÓN	04/07/18	FNAV	FNAV	GVILL	

LISTA DE REVISIONES

CONTRATISTA : SUPERCEMENTO

TECNOLOGO: MSF Tech

CLIENTE : ADMINISTRACION INFRAESTUCTURAS FERROVIARIAS S.E.

OBRA : BERAZATEGUI – LA PLATA LP 17/2016 ADECUACION DE SEÑALAMIENTO

DESCRIPCIÓN: ESQUEMA MIMICO TOLOSA

PLANO N : 017-16-C-S-LGR-022-01

CODIGO INTERNO: 536-07-105-01-B

COMPLEMENTA AL PLANO N :

REEMPLAZA AL PLANO :

DIBUJO: FNAV

ESCALA : 1:4

FECHA: 04/07

REV.: 00

HOJA: 2

017-16-C-S-LGR-022-01.dwg