



 

NOTA: LOS PÓRTICOS A MODIFICAR INDICADOS INVADEN EL GÁLIBO DE LA TRAZA DEL PROYECTO. AL MENOS SE DEBERÁ MODIFICAR LA UBICACIÓN DE LOS POSTES CON COORDENADAS IGN P1; P2 Y P3;P4, DADA LA IMPOSIBILIDAD DE MODIFICAR EL PROYECTO ACORDE AL EMPLAZAMIENTO ACTUAL DE DICHS POSTES.

POSTES	N	E	X	Y
P1	6139647.68	6410836.85	154.14	333.95
P2	6139633.73	6410824.11	153.85	315.06
P3	6139622.02	6410817.85	158.84	339.28
P4	6139603.36	6410857.49	158.98	314.47

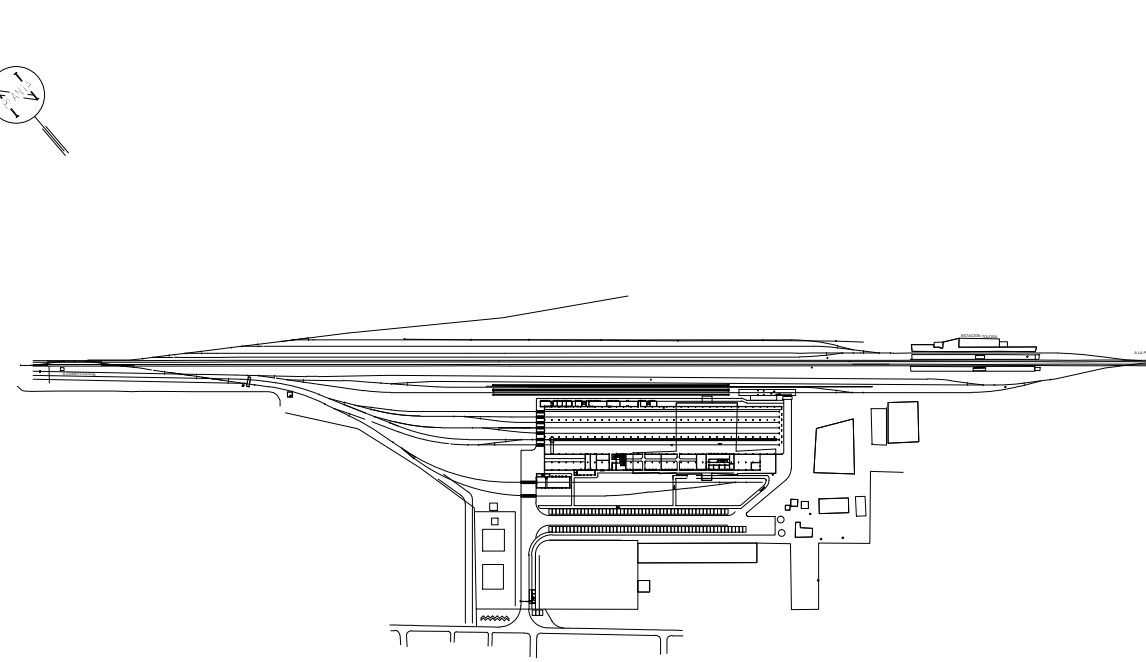

PLANO DE UBICACION (sin escala)

NOTAS

REFERENCIAS

- CI-TOL-PL-VIA-003
- CI-TOL-PL-VIA-004
- CI-TOL-PL-ARQ-003
- EM-TOL-ET-E00-002
- CI-TOL-PL-GEN-001
- CI-TOL-PL-GEN-002
- CI-TOL-PL-HAE-008
- CI-TOL-PL-HAE-012

- VIAS ELECTRIFICADAS CON CATENARIA
- VIAS SIN ELECTRIFICAR
- VIAS PRINCIPALES
- VIAS EXISTENTES EN FUNCIONAMIENTO
- SECCIONES DE VIAS Y/O VIAS DE PROYECTO
- ADV DE PROYECTO
- TOPOS DE FIN DE VIA
- EDIFICIOS Y CONSTRUCCIONES EXISTENTES
- COTA GEODESICA

2	5/07/2017	PROYECTO EJECUTIVO PARA APROBACION	ELABORO	REVISO	APROBO	Y B. UEC
0	08/03/2015	PARA PLEGIO	ELABORO	REVISO	APROBO	Y B. UEC

REPÚBLICA ARGENTINA - MINISTERIO DE TRANSPORTE
UNIDAD EJECUTORA CENTRAL

esuco	DEPOSITO FERROVIARIO TOLOSA	Escales: 1:1000
UNIDAD EJECUTORA CENTRAL	DEPOSITO TOLOSA LAYOUT GENERAL DE PLANTA	PLANO N° CI-TOL-PL-VIA-001
Ministerio de Transporte	Fecha: 05/07/2017	Hoja 1 de 1
Presidencia de la Nación	Revisión: 2	1869x 394