
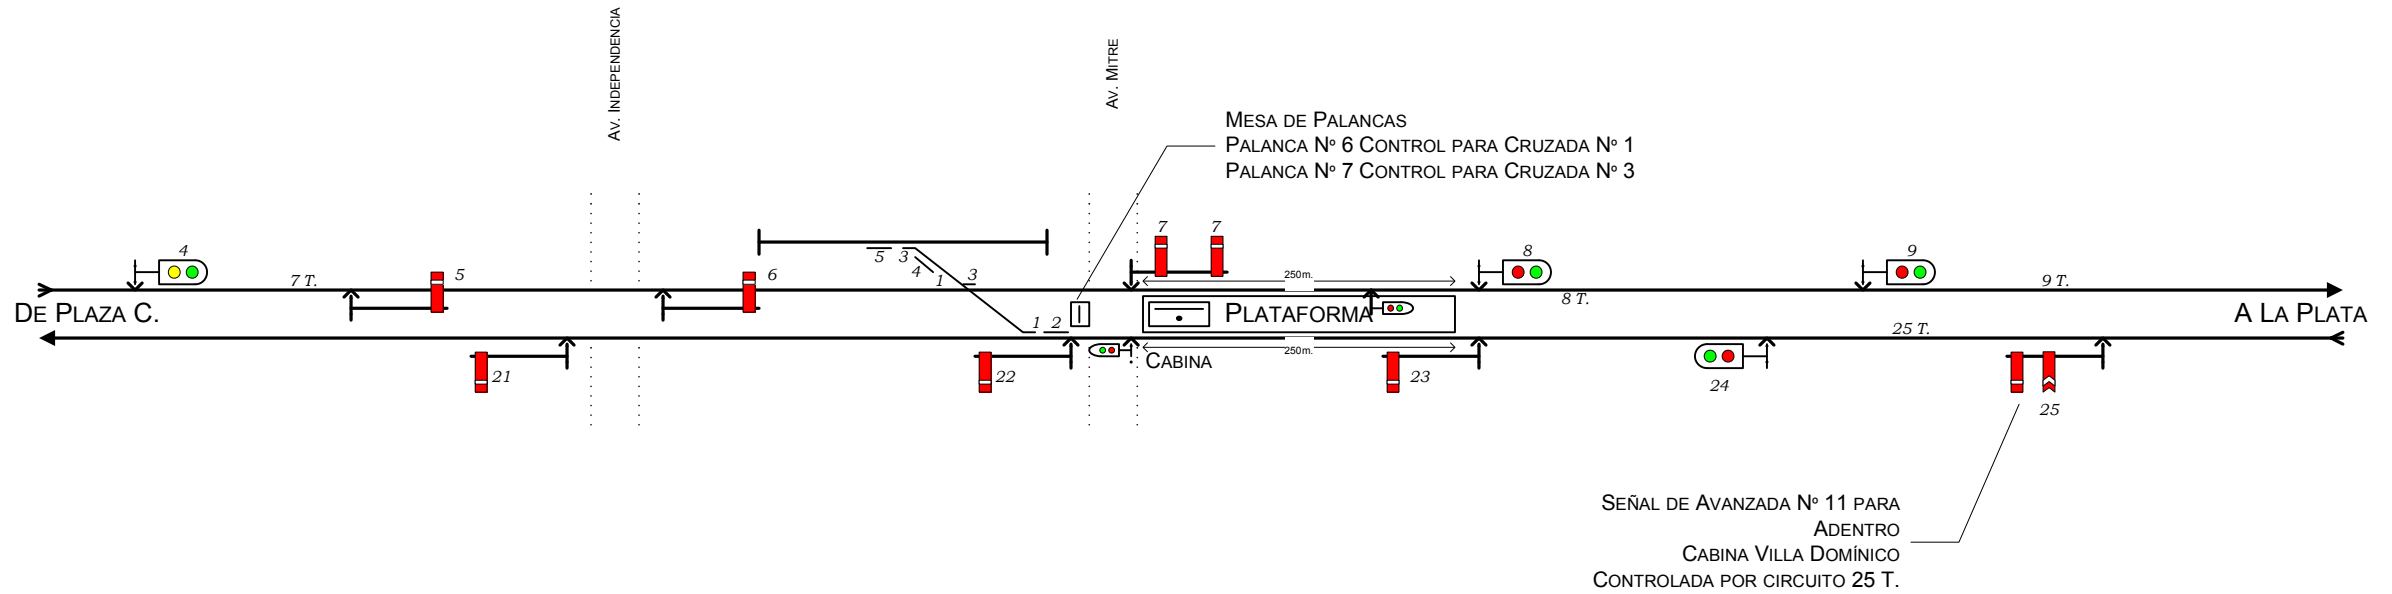


SARANDÍ



KM. 7,769

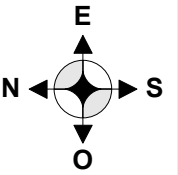

PALANCAS DE REPUESTO: 1 - 2 - 3 - 10 - 11 - 12 - 15 - 16 - 17 - 18 -
19

ESTACIÓN SARANDÍ	
ESQUEMA DE CAMBIOS Y SEÑALES	26/06/99
RICARDO A. AMODIO - AREA TRANSPORTE C.C.	5.1

KM. 9,996

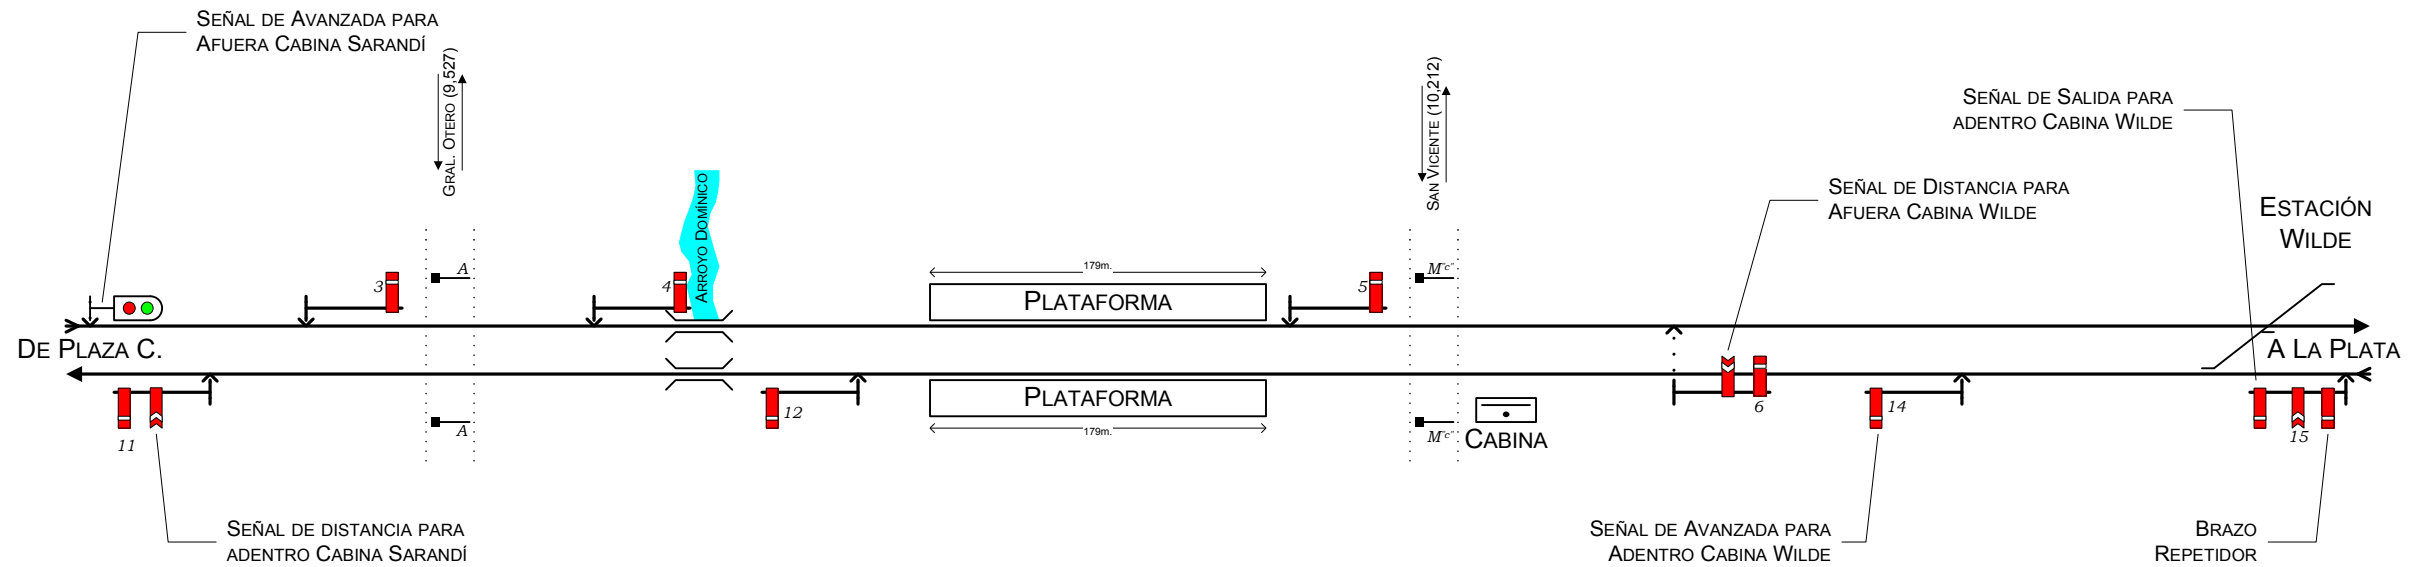
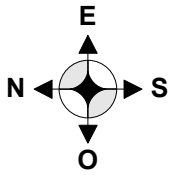


LLAVE DE BARRERAS N° 1
LLAVE DE CLAUSURA N° 7
PALANCAS DE REPUESTO: 8 - 9 - 11

ESTACIÓN VILLA DOMÍNICO	
ESQUEMA DE CAMBIOS Y SEÑALES	26/06/99
RICARDO A. AMODIO - AREA TRANSPORTE C.C.	5.2

WILDE

KM. 11,399

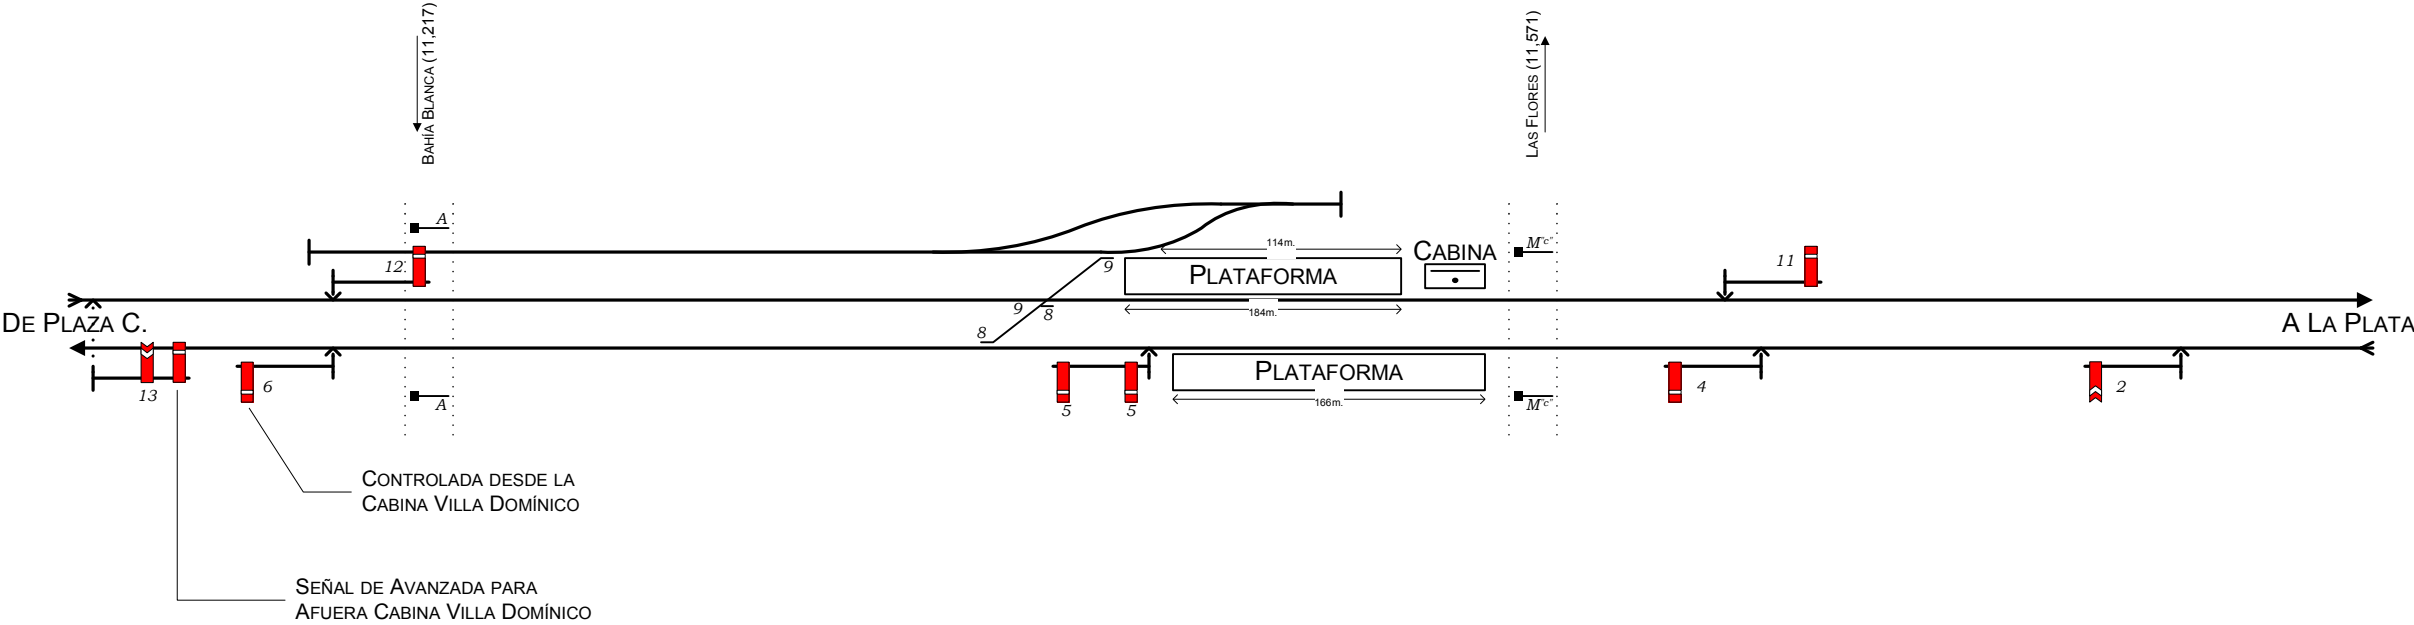
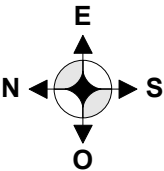


PALANCA N° 1: CONTROL BARRERA
PALANCAS DE REPUESTO: 7

ESTACIÓN WILDE	
ESQUEMA DE CAMBIOS Y SEÑALES	26/06/99
RICARDO A. AMODIO - AREA TRANSPORTE C.C.	5.3

BERNAL

KM. 14,578

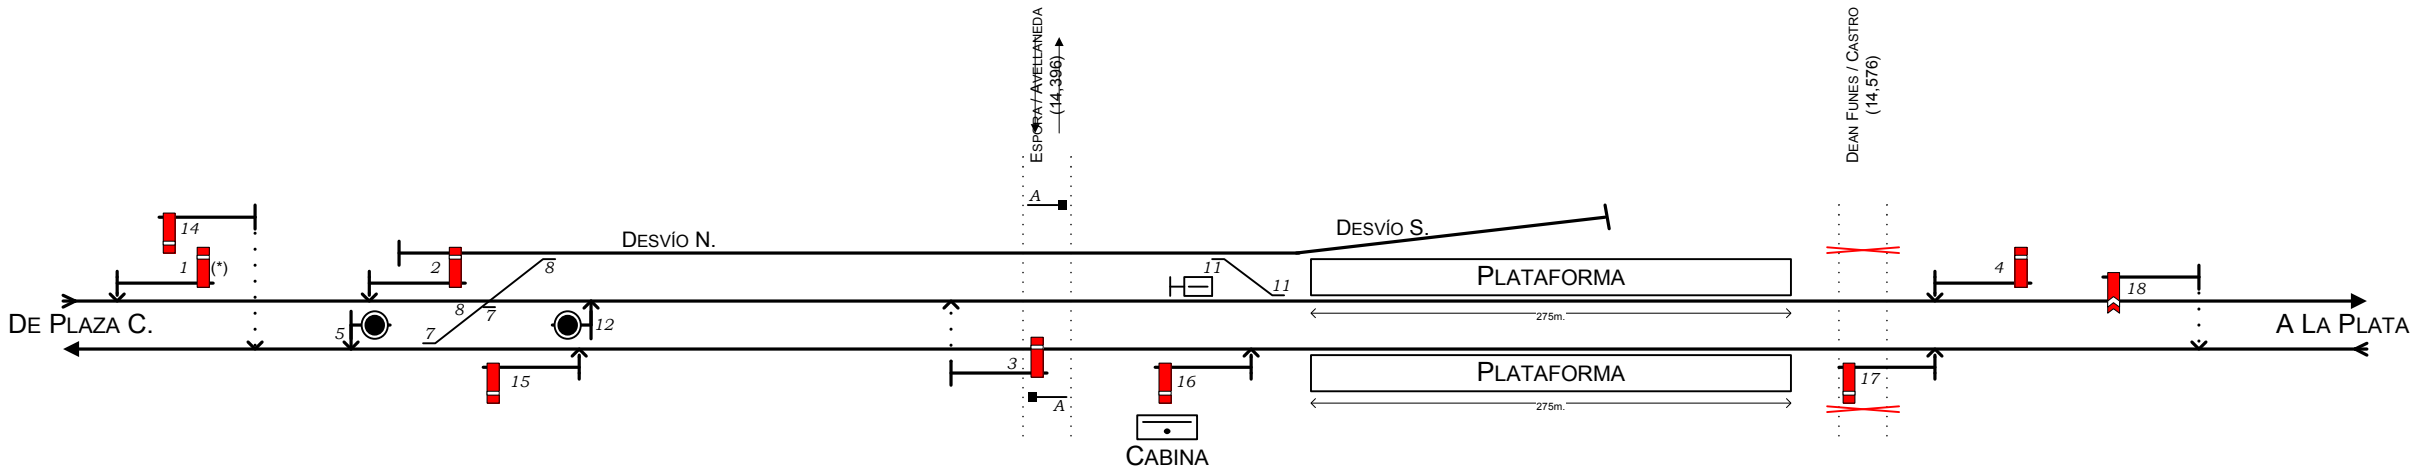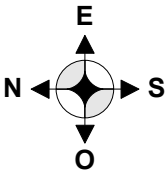



(*) Ex SEÑAL DE DISTANCIA CONVERTIDA EN ABSOLUTA

PALANCAS DE REPUESTO: 9 - 10 - 13

ESTACION BERNAL	
ESQUEMA DE CAMBIOS Y SEÑALES	26/06/99
RICARDO A. AMODIO - AREA TRANSPORTE C.C.	5.4

QUILMES



KM. 14,578

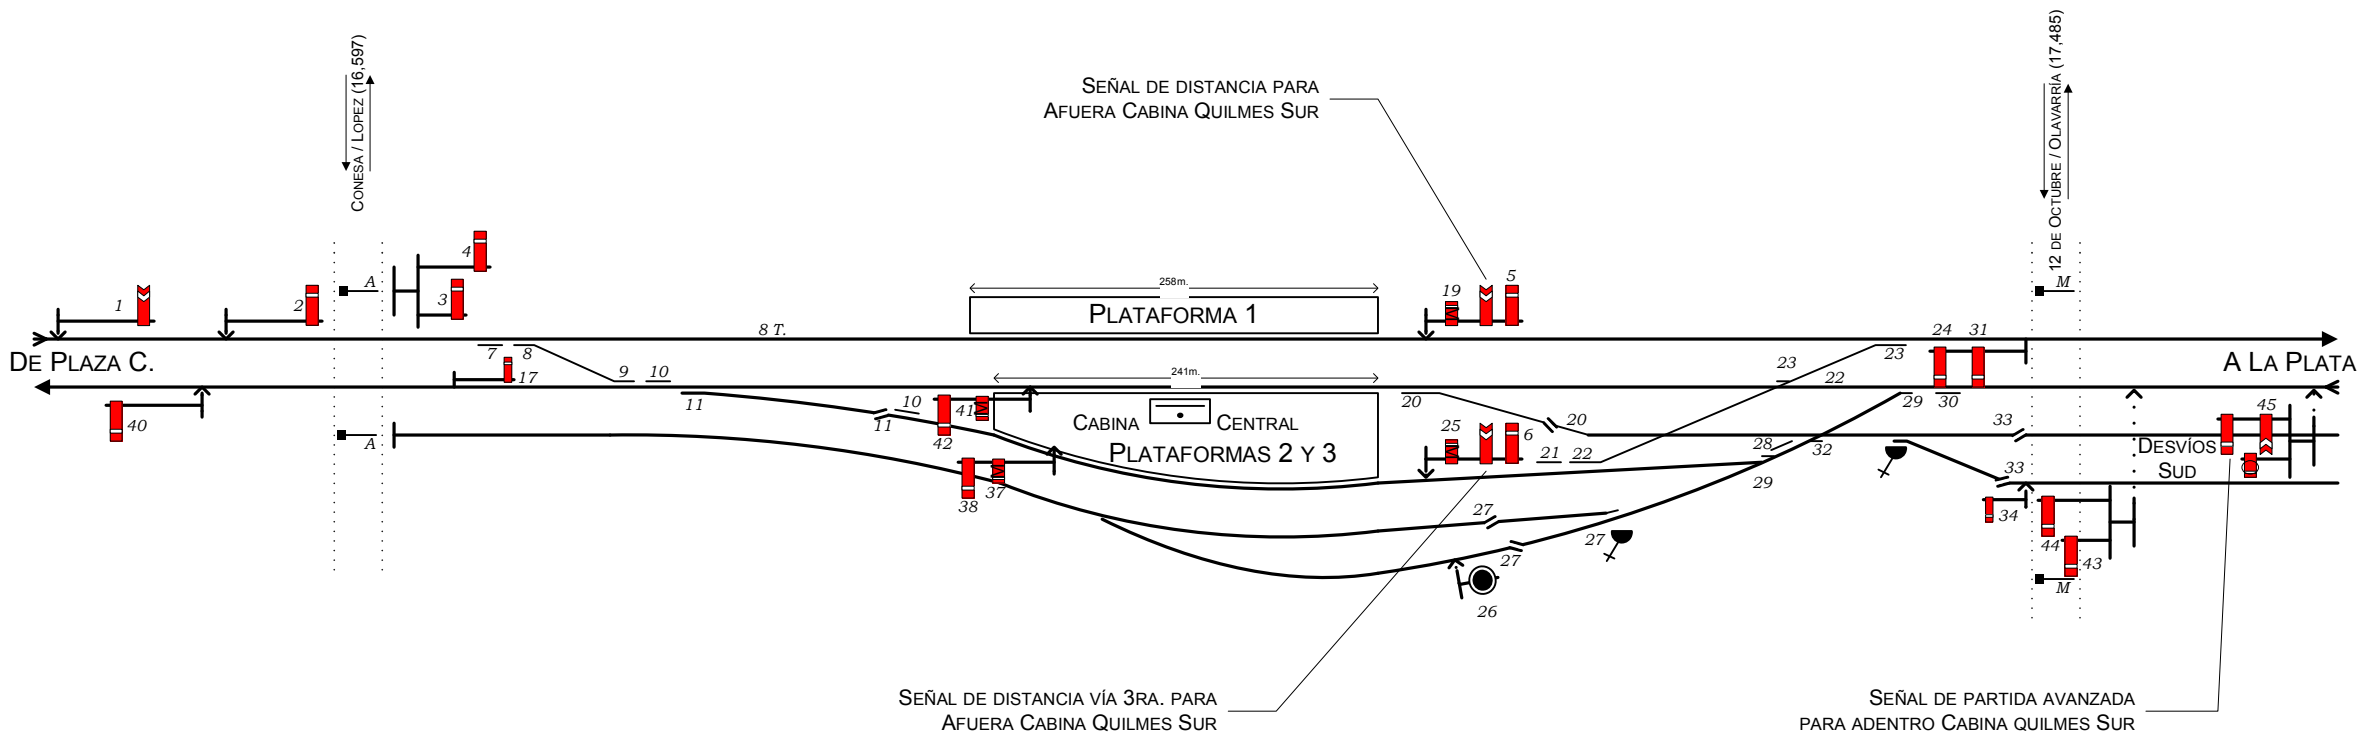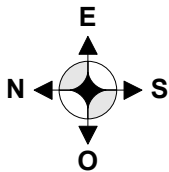

ESTACION QUILMES	
ESQUEMA DE CAMBIOS Y SEÑALES	7/09/1999
RICARDO A. AMODIO - AREA TRANSPORTE C.C.	5.5

PALANCAS DE REPUESTO: 9 - 10 - 13



KM. XX

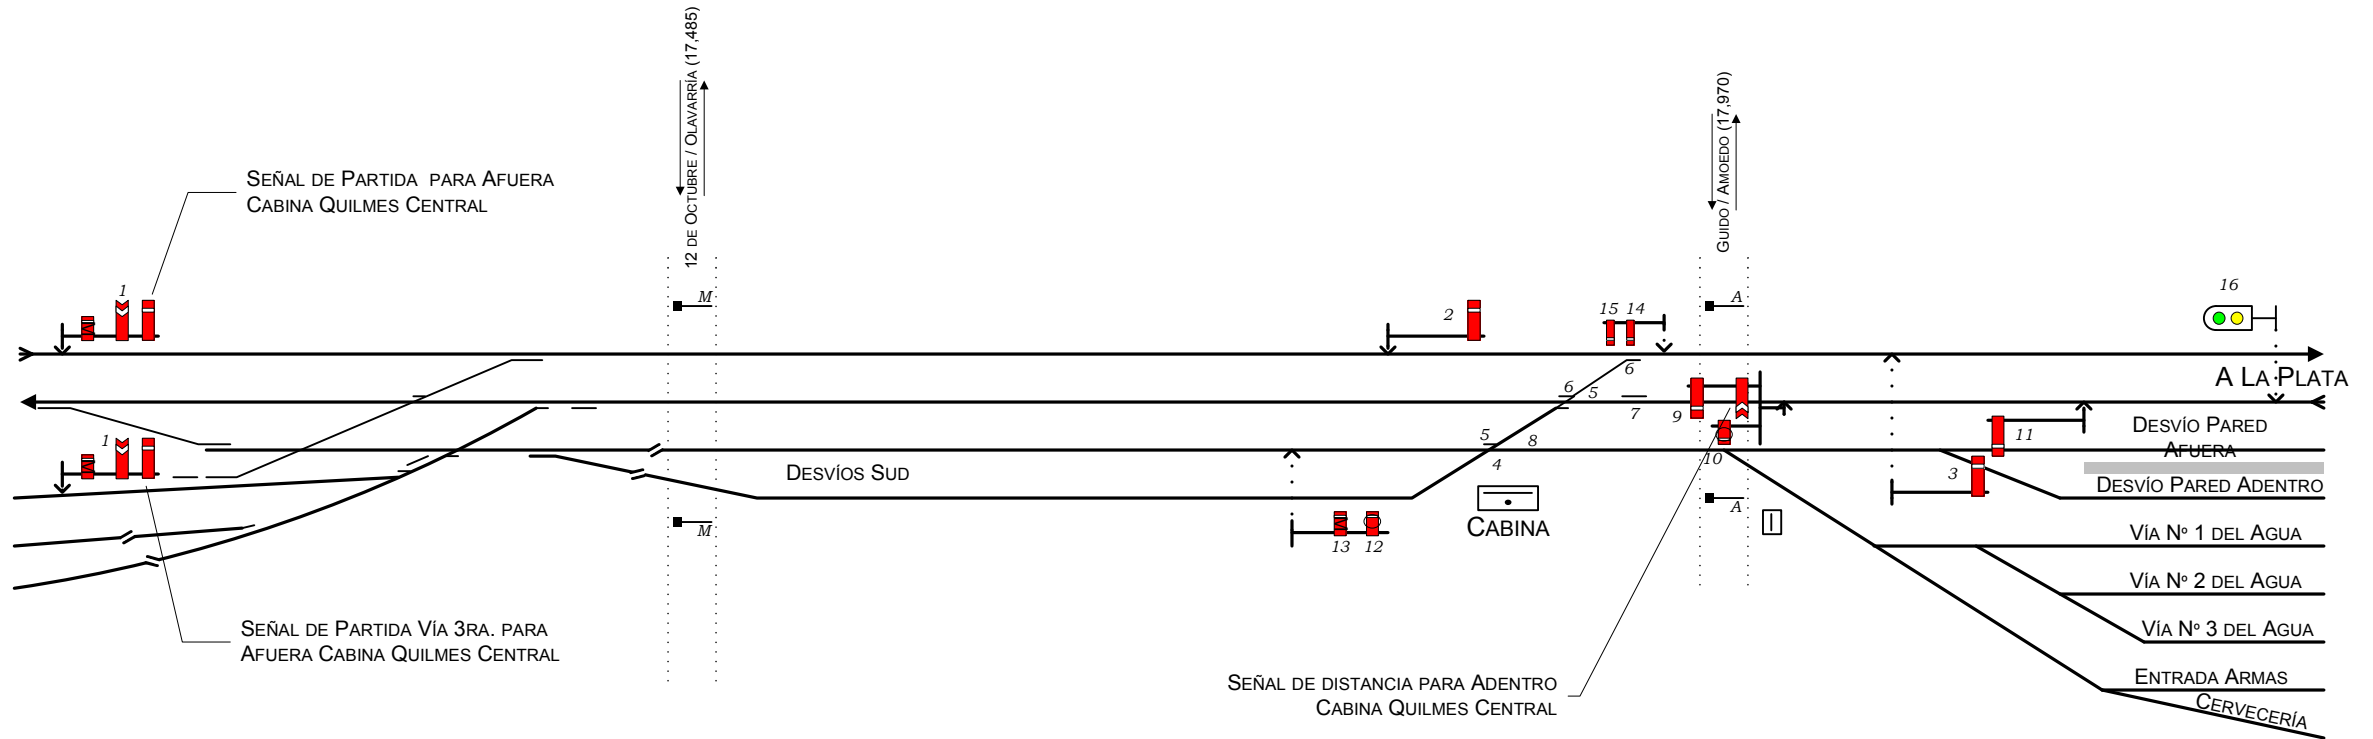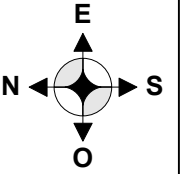

CABINA QUILMES SUR	
ESQUEMA DE CAMBIOS Y SEÑALES	25/09/2000
RICARDO A. AMODIO - AREA TRANSPORTE C.C.	5.6

EZPELETA

KM. 21,230

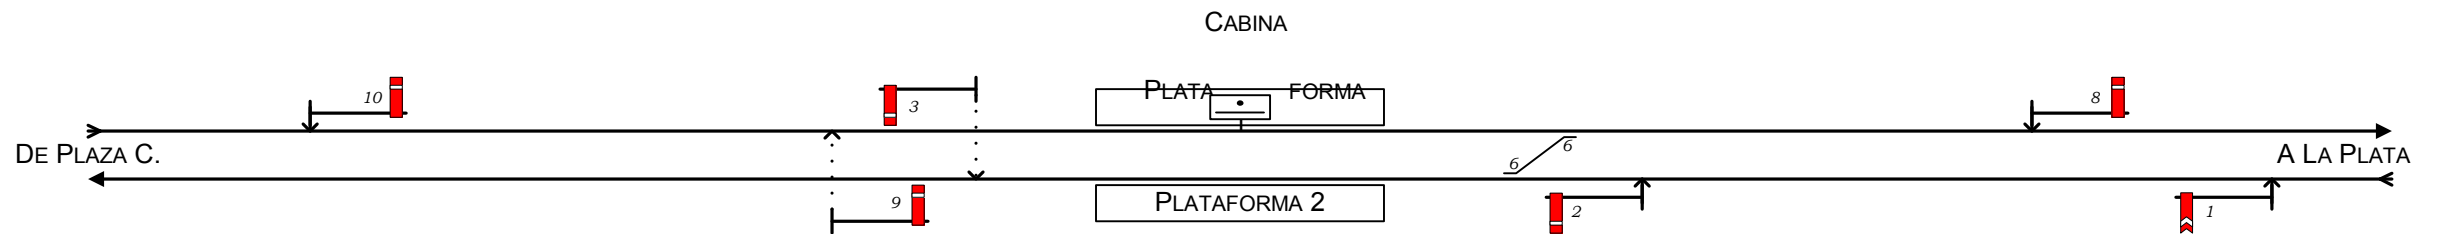
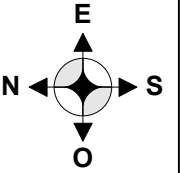


LLAVE DE CLAUSURA N° 7
PALANCAS DE REPUESTO:

ESTACIÓN EZPELETA	
ESQUEMA DE CAMBIOS Y SEÑALES	26/06/99
RICARDO A. AMODIO - AREA TRANSPORTE C.C.	5.7

BERAZATEGUI

KM. 23,799

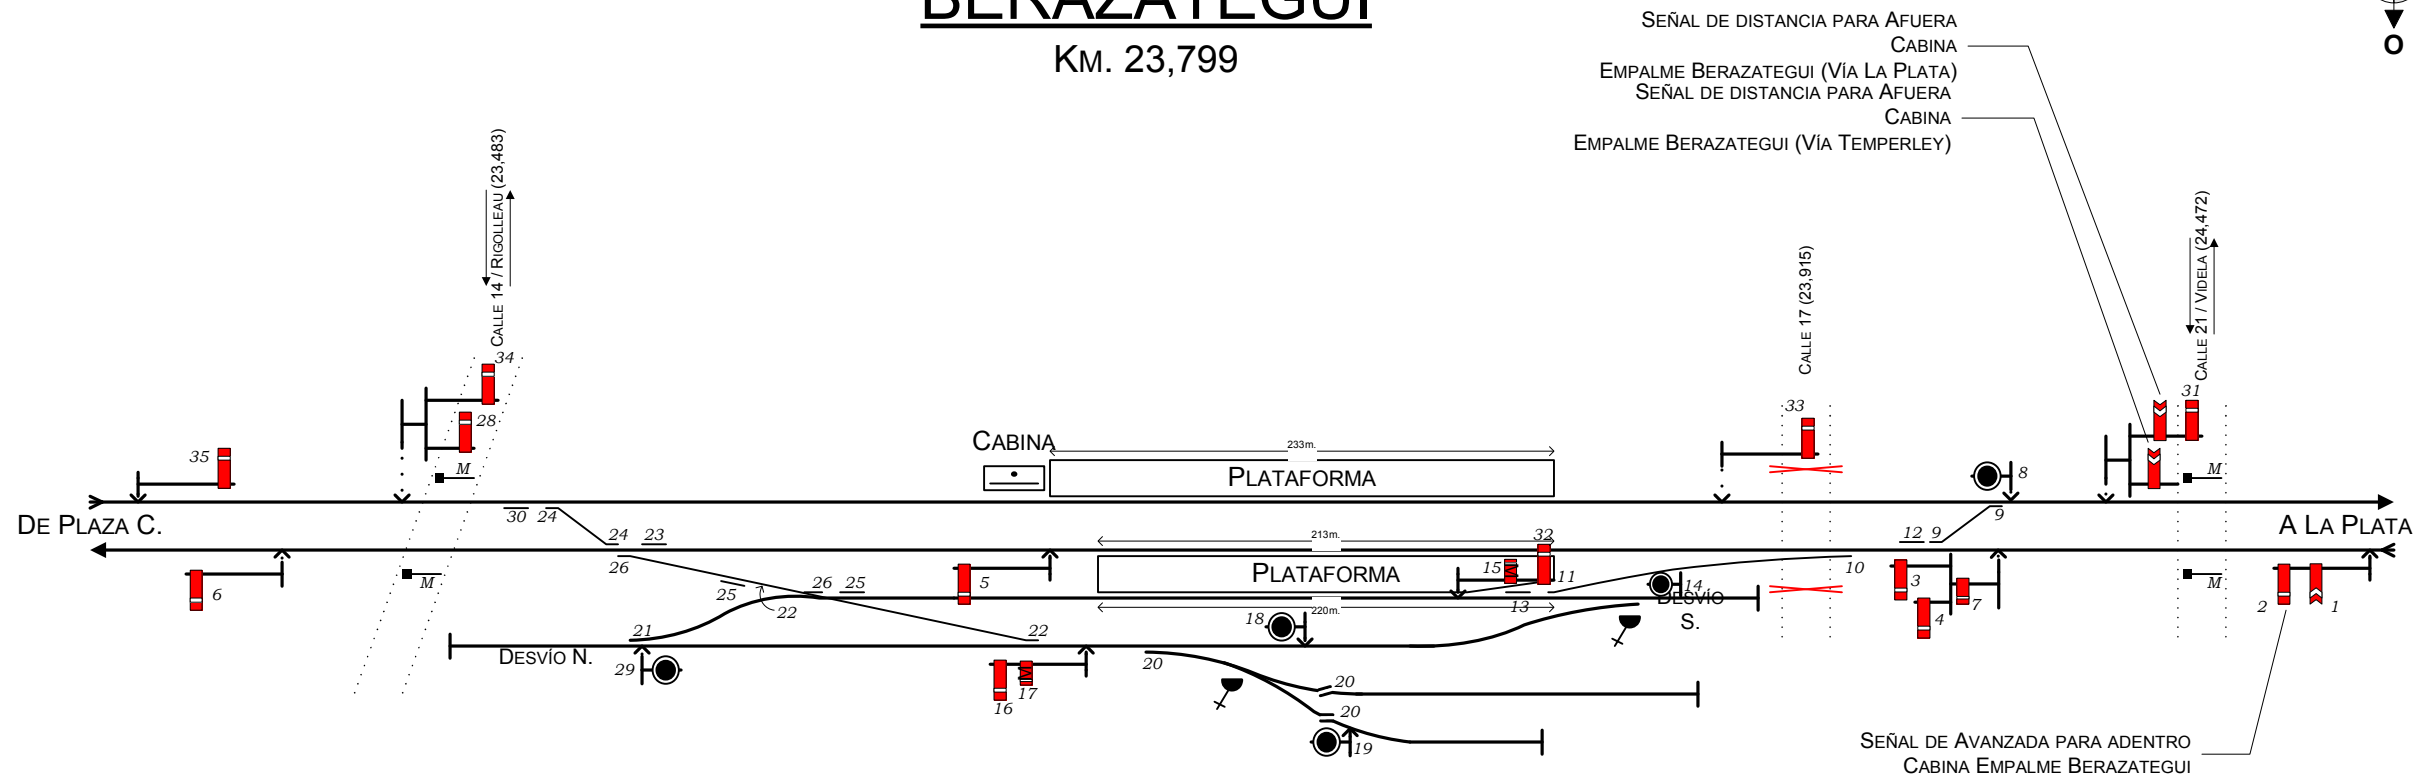
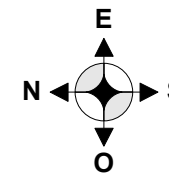


PALANCAS DE REPUESTO: 3

ESTACIÓN BERAZATEGUI	
ESQUEMA DE CAMBIOS Y SEÑALES	26/07/99
RICARDO A. AMODIO - AREA TRANSPORTE C.C.	5.8

EMPALME BERAZATEGUI

Km. 25,004

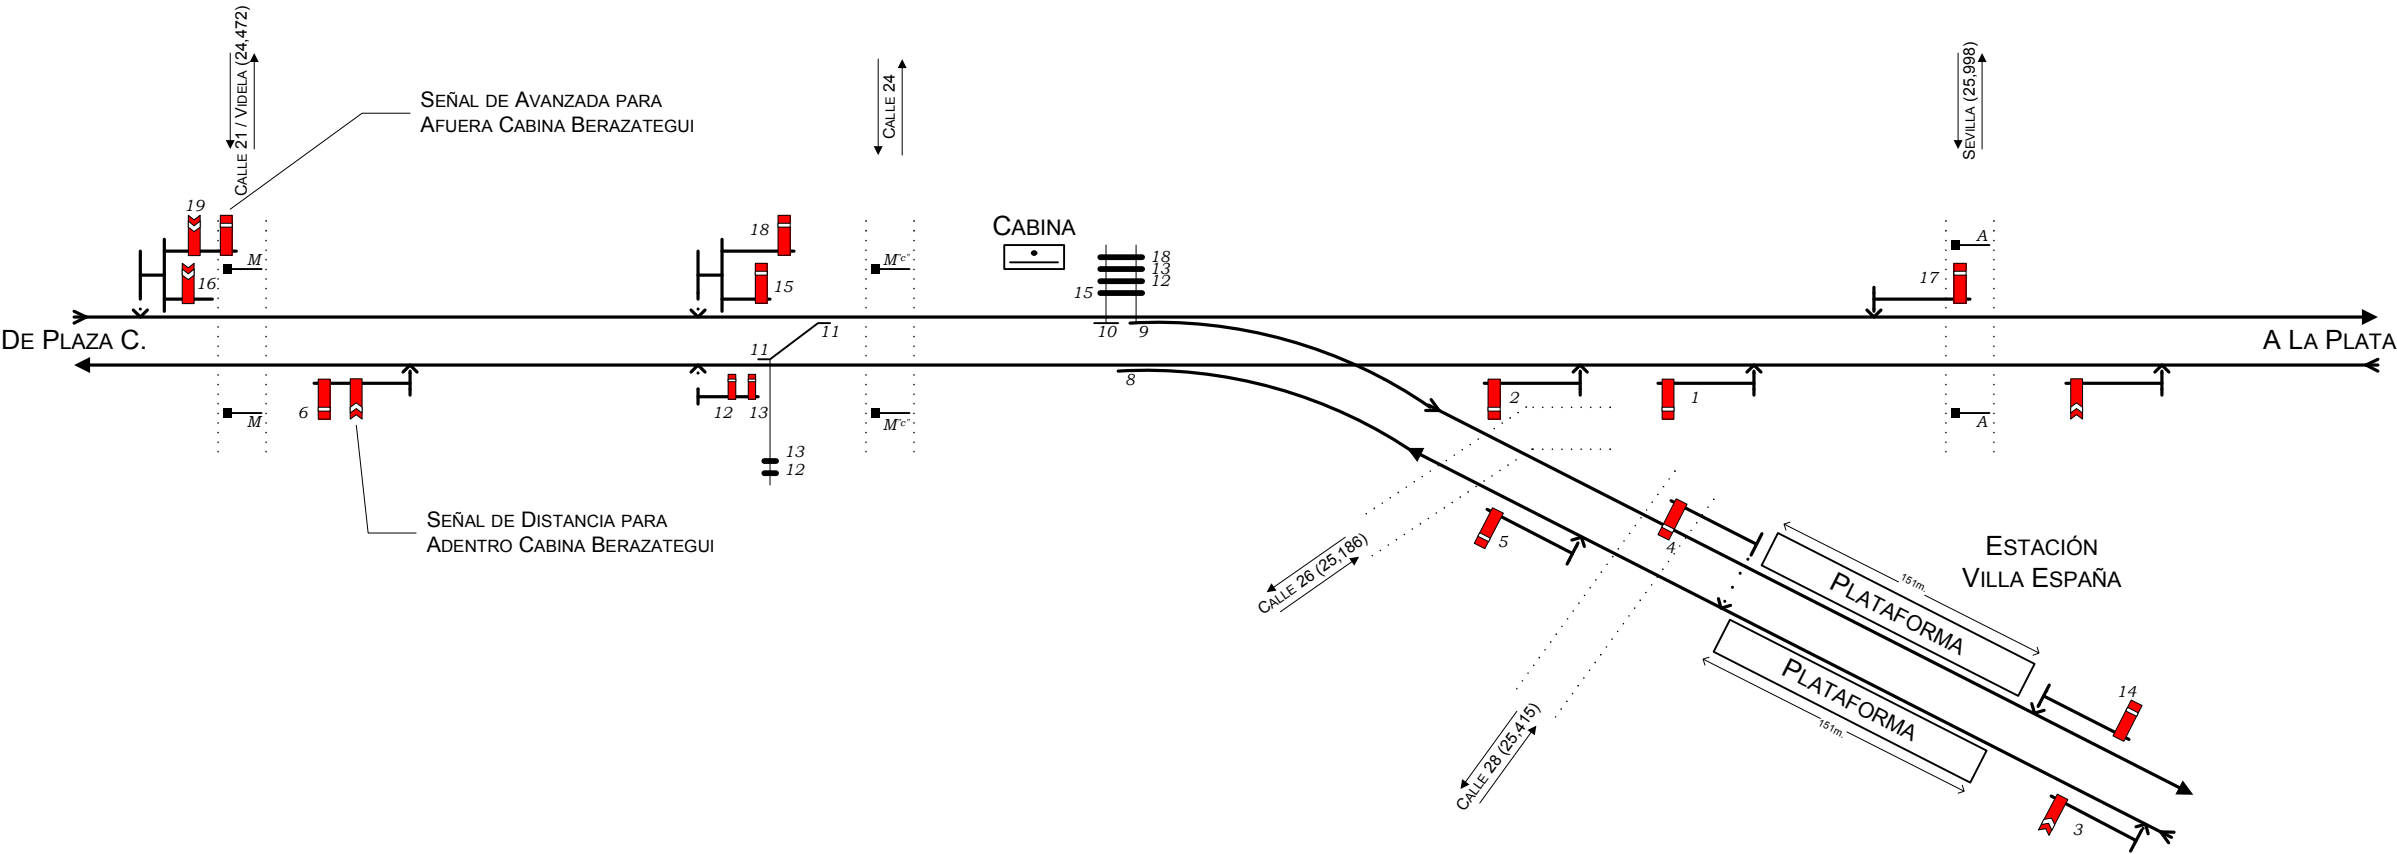
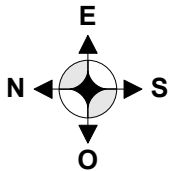


PALANCA Nº 20: CONTROL BARRERAS
PALANCAS DE REPUESTO: 0

EMPALME BERAZATEGUI	
ESQUEMA DE CAMBIOS Y SEÑALES	26/06/99
RICARDO A. AMODIO - AREA TRANSPORTE C.C.	5.9

G. E. HUDSON

KM. 29,520

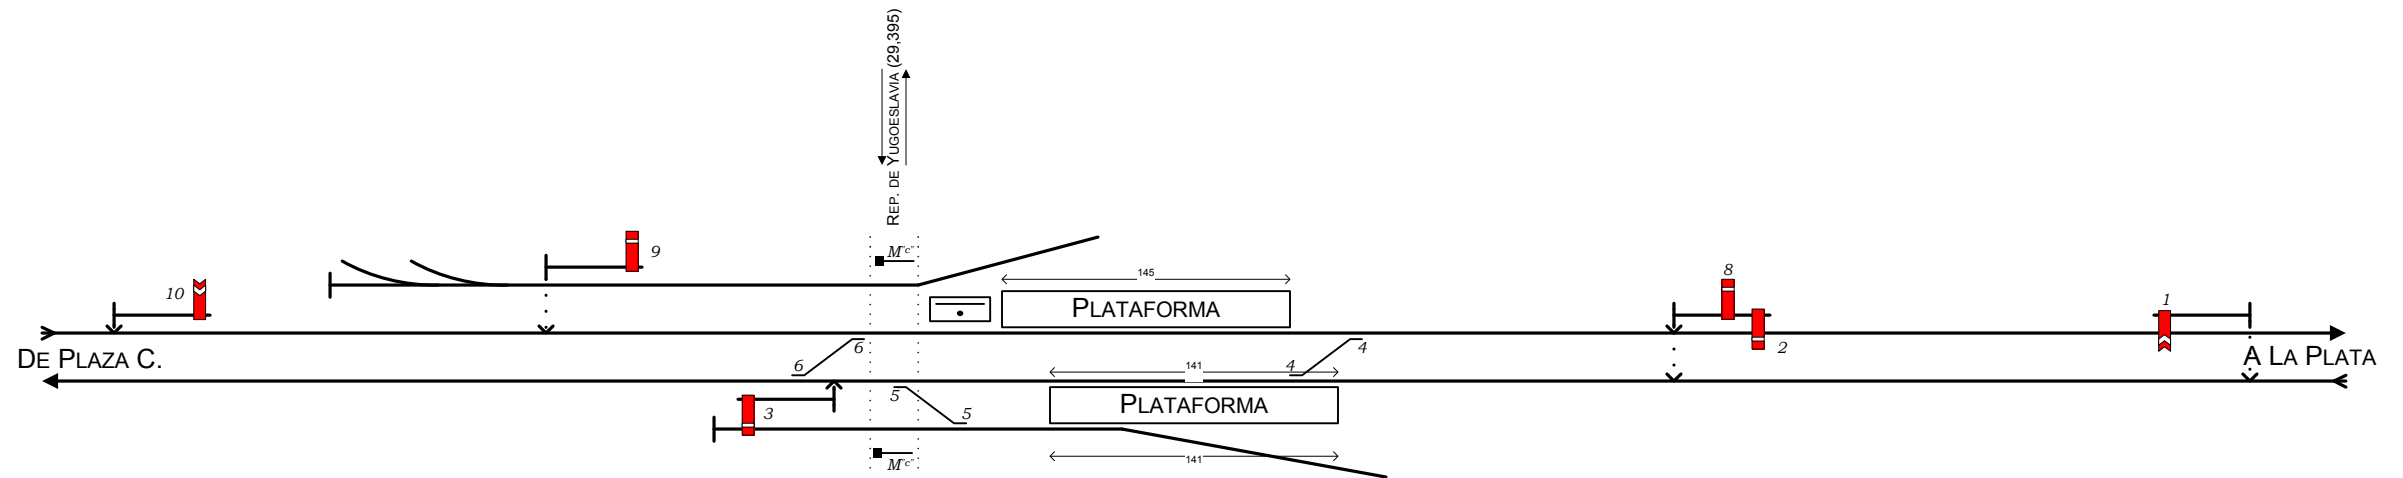
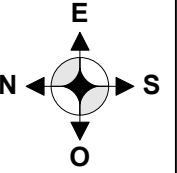


PALANCAS DE REPUESTO: 0

ESTACIÓN G. E. HUDSON	
ESQUEMA DE CAMBIOS Y SEÑALES	26/06/99
RICARDO A. AMODIO - AREA TRANSPORTE C.C.	5.10

VILLA ELISA



KM. 39,333

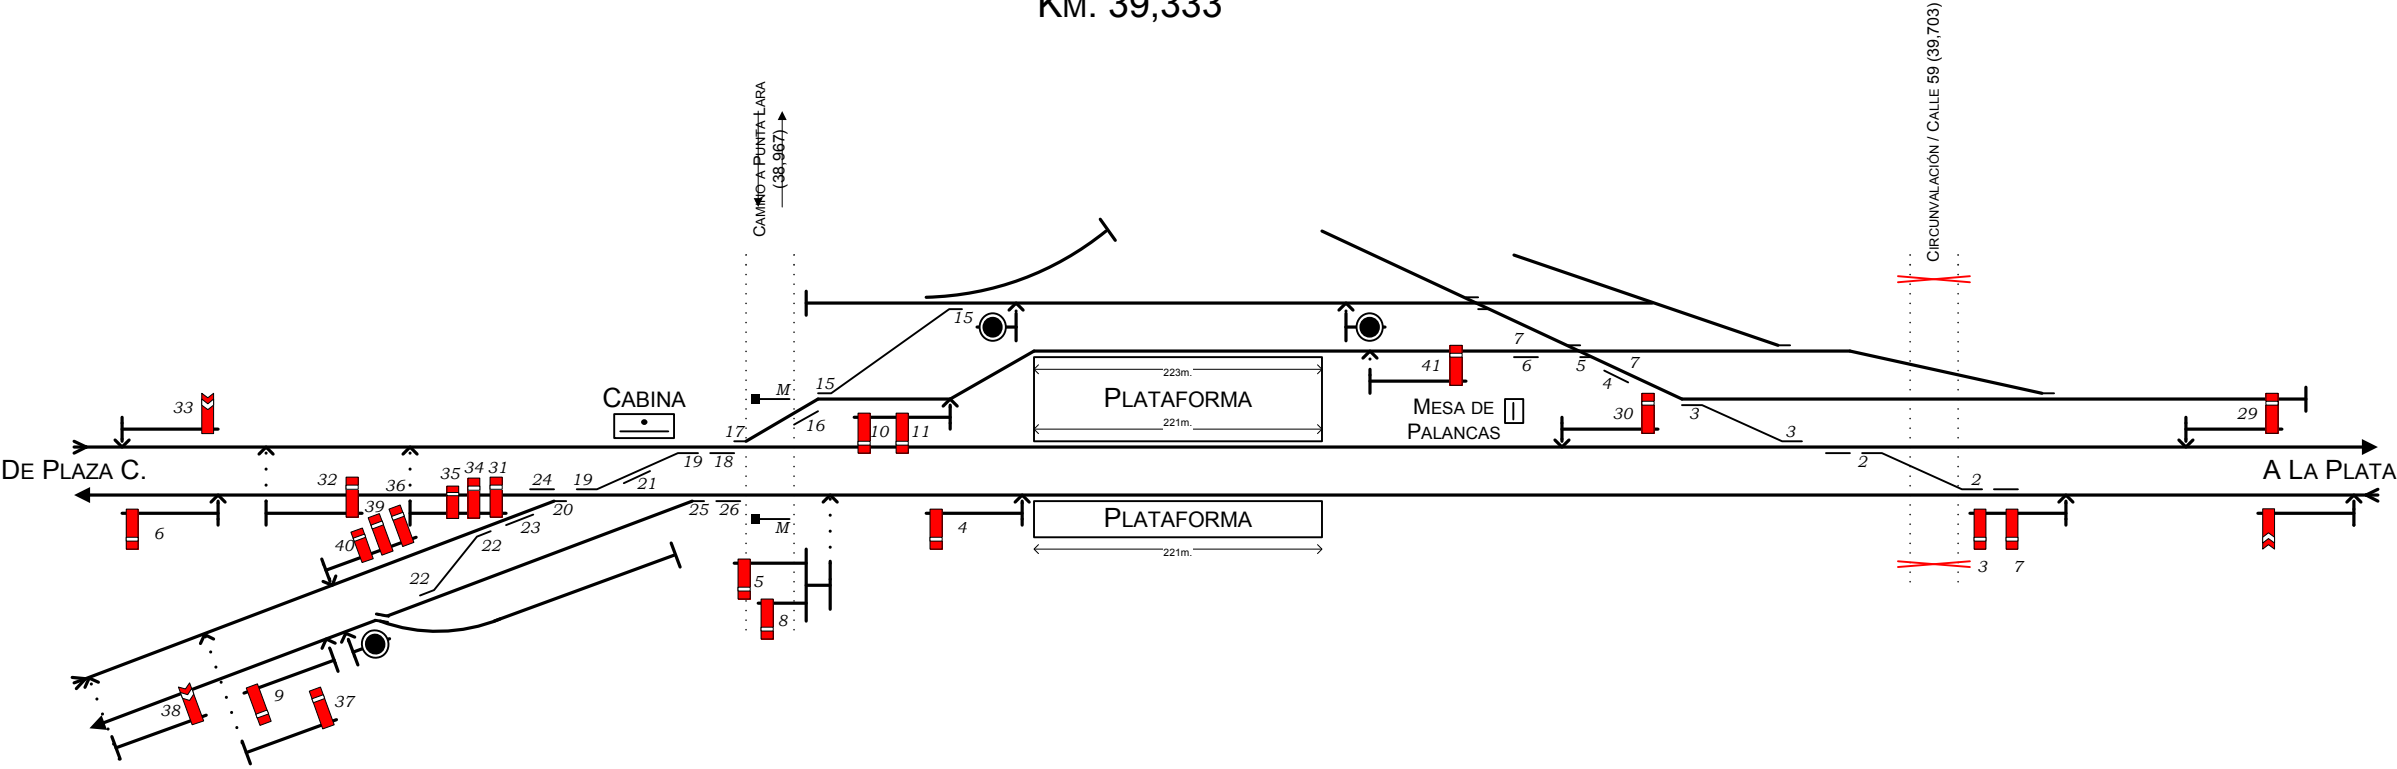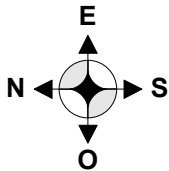

PALANCAS DE REPUESTO: 24 - 27 - 28 - 29

ESTACIÓN VILLA ELISA	
ESQUEMA DE CAMBIOS Y SEÑALES	26/06/99
RICARDO A. AMODIO - AREA TRANSPORTE C.C.	5.11

CITY BELL
KM. 42,866
(ACTUALMENTE CLAUSURADA)

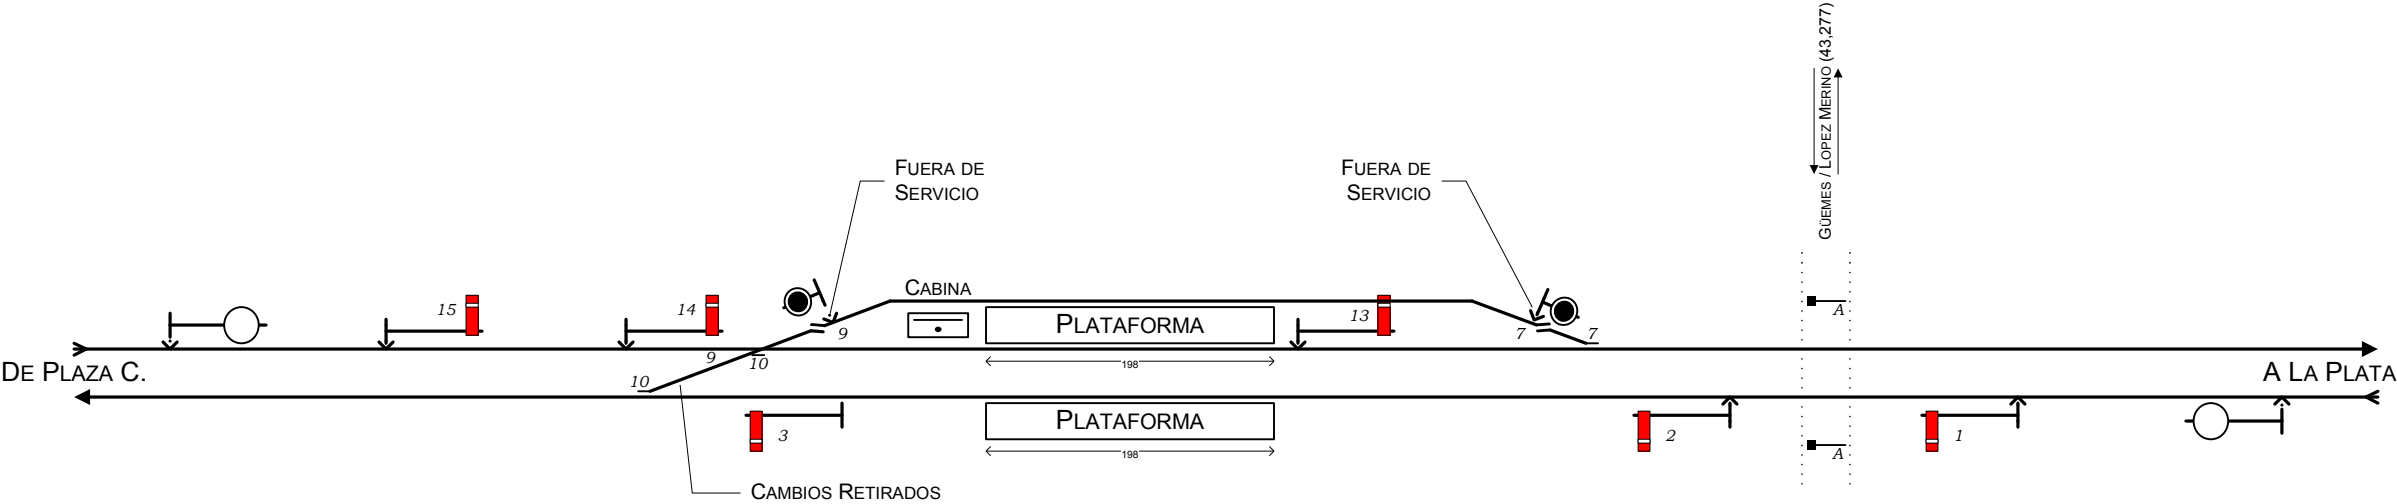
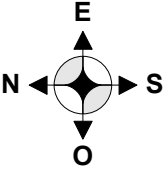


PALANCAS DE CLAUSURA: N° 8 CON CERRADURA
ANNETTS
PALANCAS DE REPUESTO: 4 - 5 - 6 - 11 - 12

ESTACIÓN CITY BELL	
ESQUEMA DE CAMBIOS Y SEÑALES	26/06/99
RICARDO A. AMODIO - AREA TRANSPORTE C.C.	5.12

RINGUELET

KM. 47,553

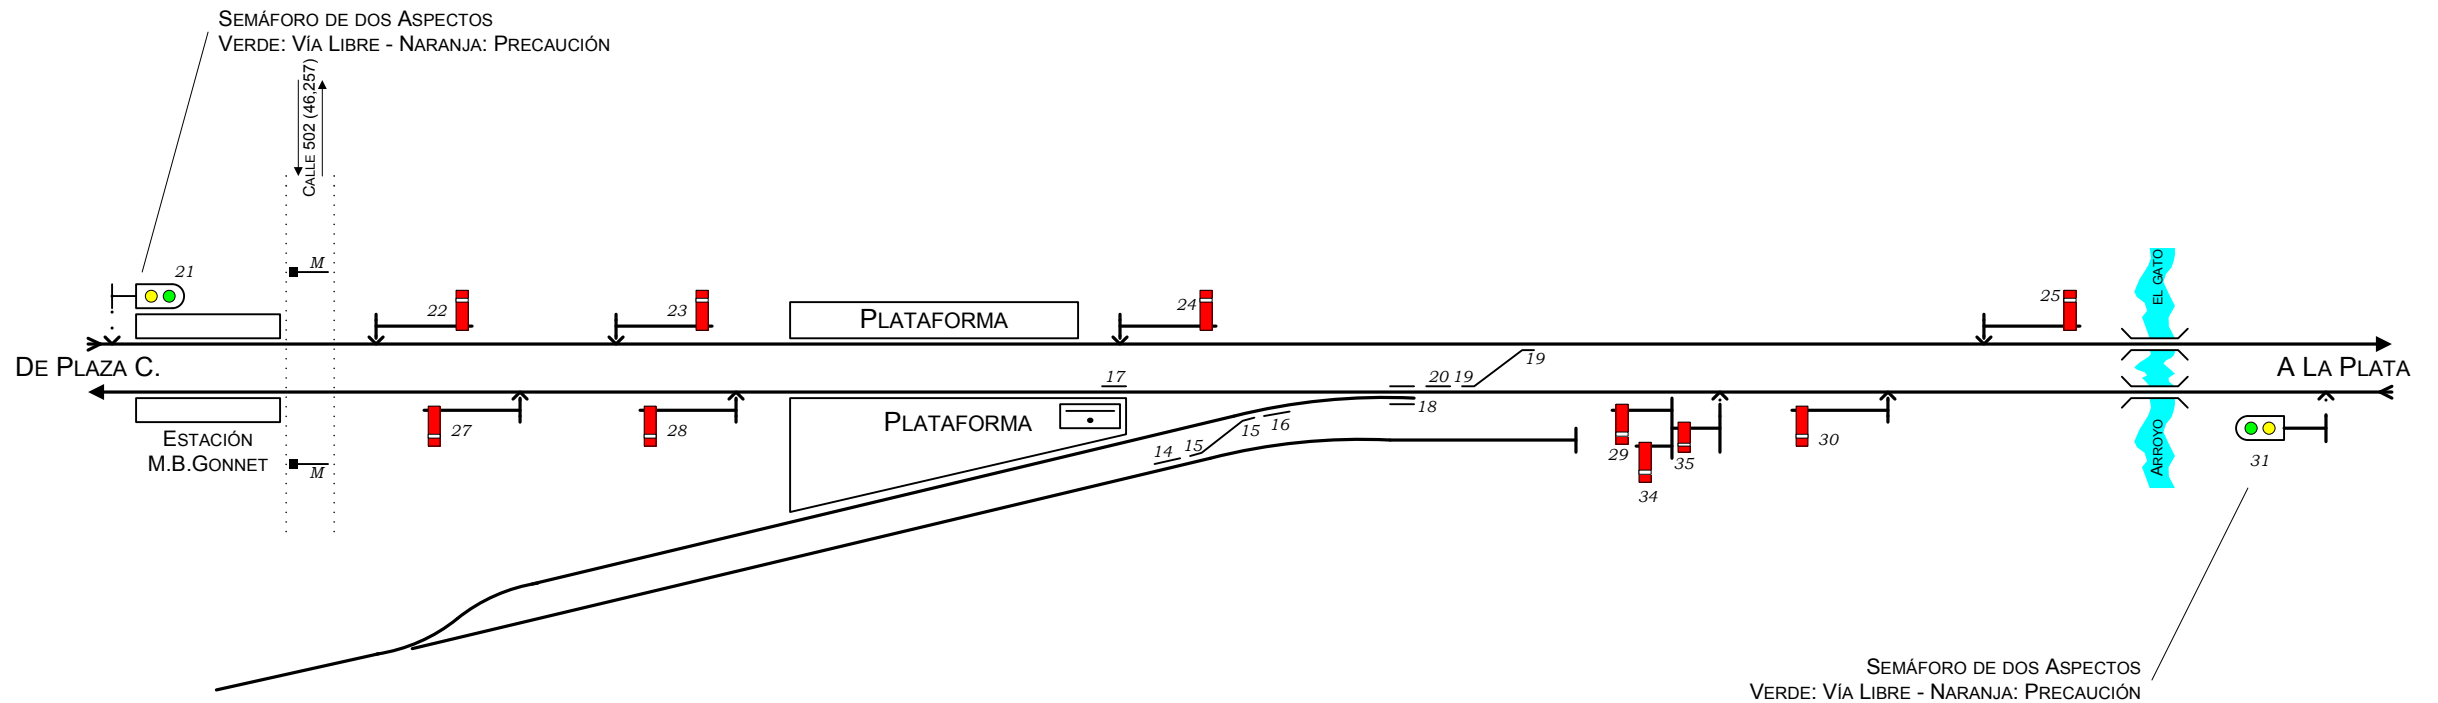
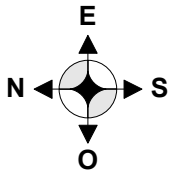


PALANCAS DE REPUESTO: 26

ESTACIÓN RINGUELET	
ESQUEMA DE CAMBIOS Y SEÑALES	24/10/2000
RICARDO A. AMODIO - AREA TRANSPORTE C.C.	5.13

TOLOSA SUD

KM. 50,555

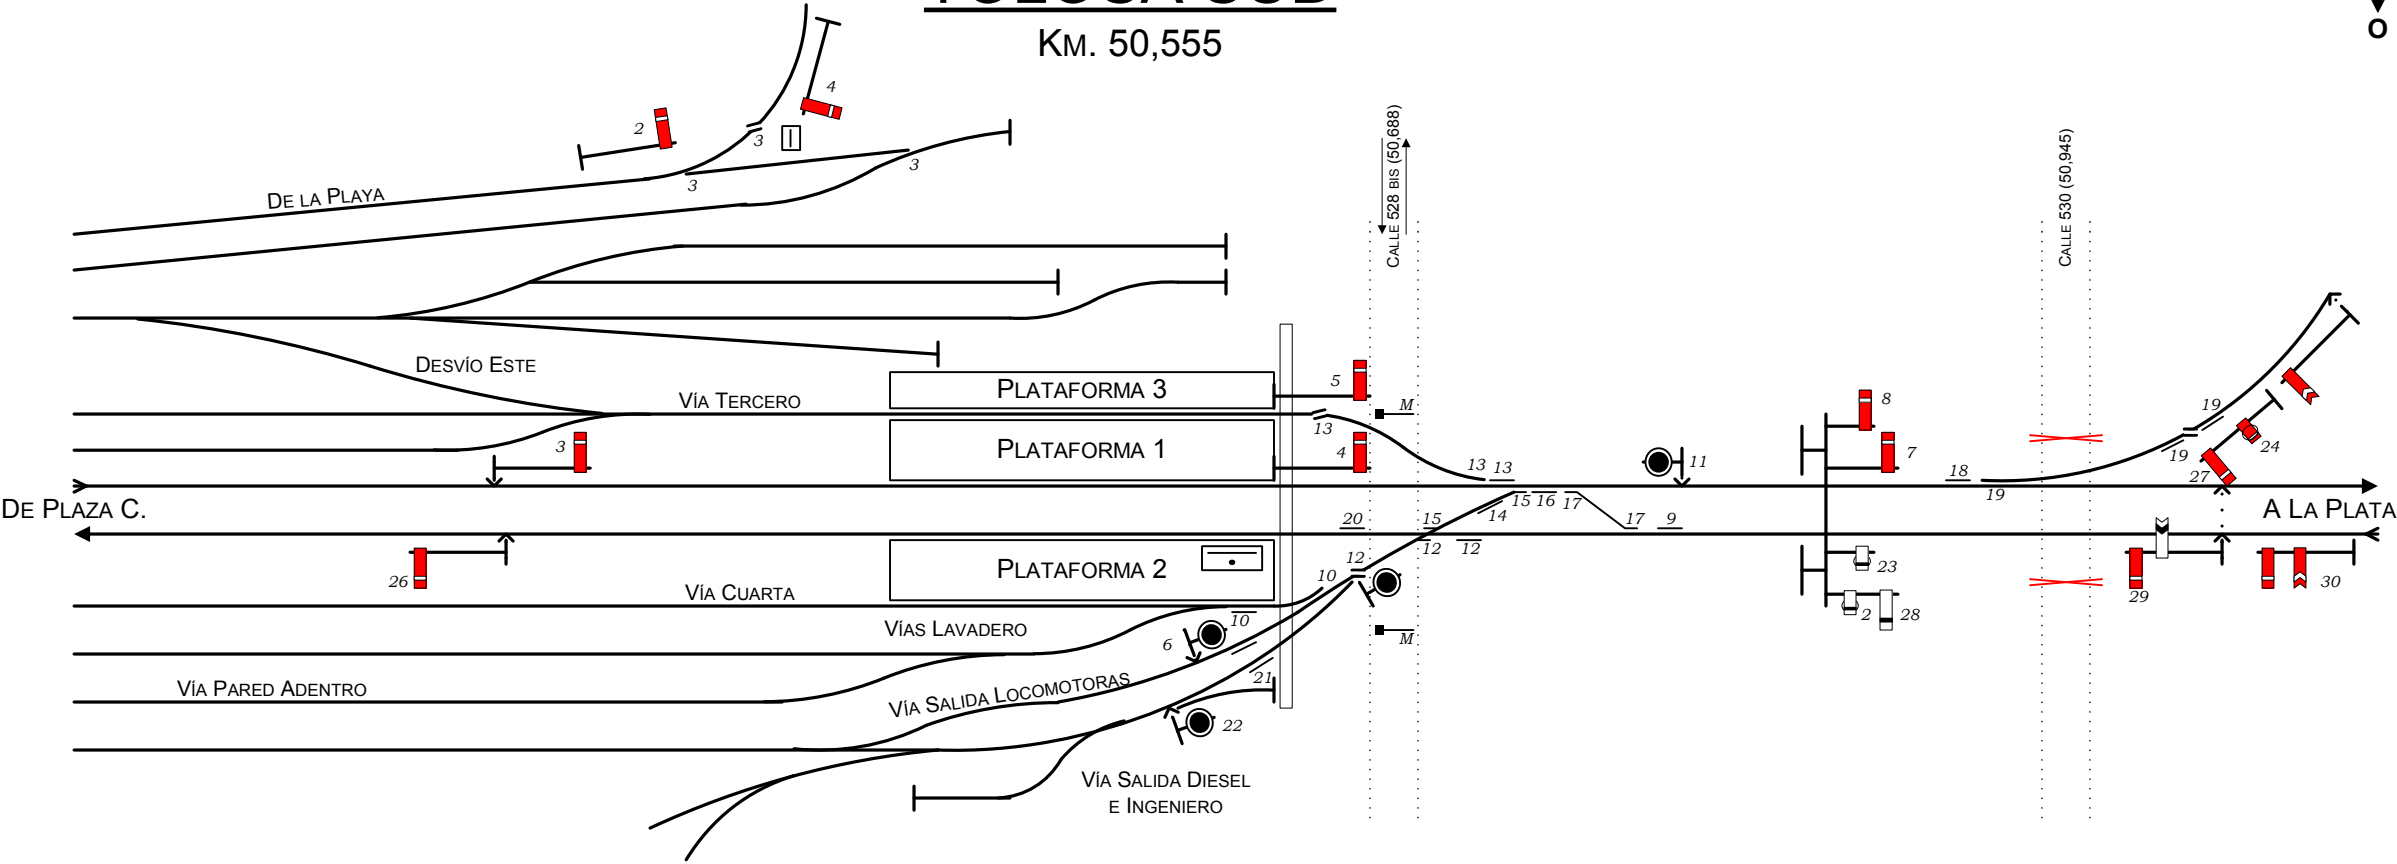
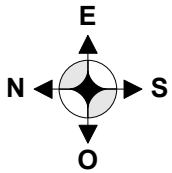


PALANCAS DE REPUESTO: 2

ESTACIÓN TOLOSA	
ESQUEMA DE CAMBIOS Y SEÑALES	3/12/2001
RICARDO A. AMODIO - AREA TRANSPORTE C.C.	5.14

KM. 52,606

KM. 52,606

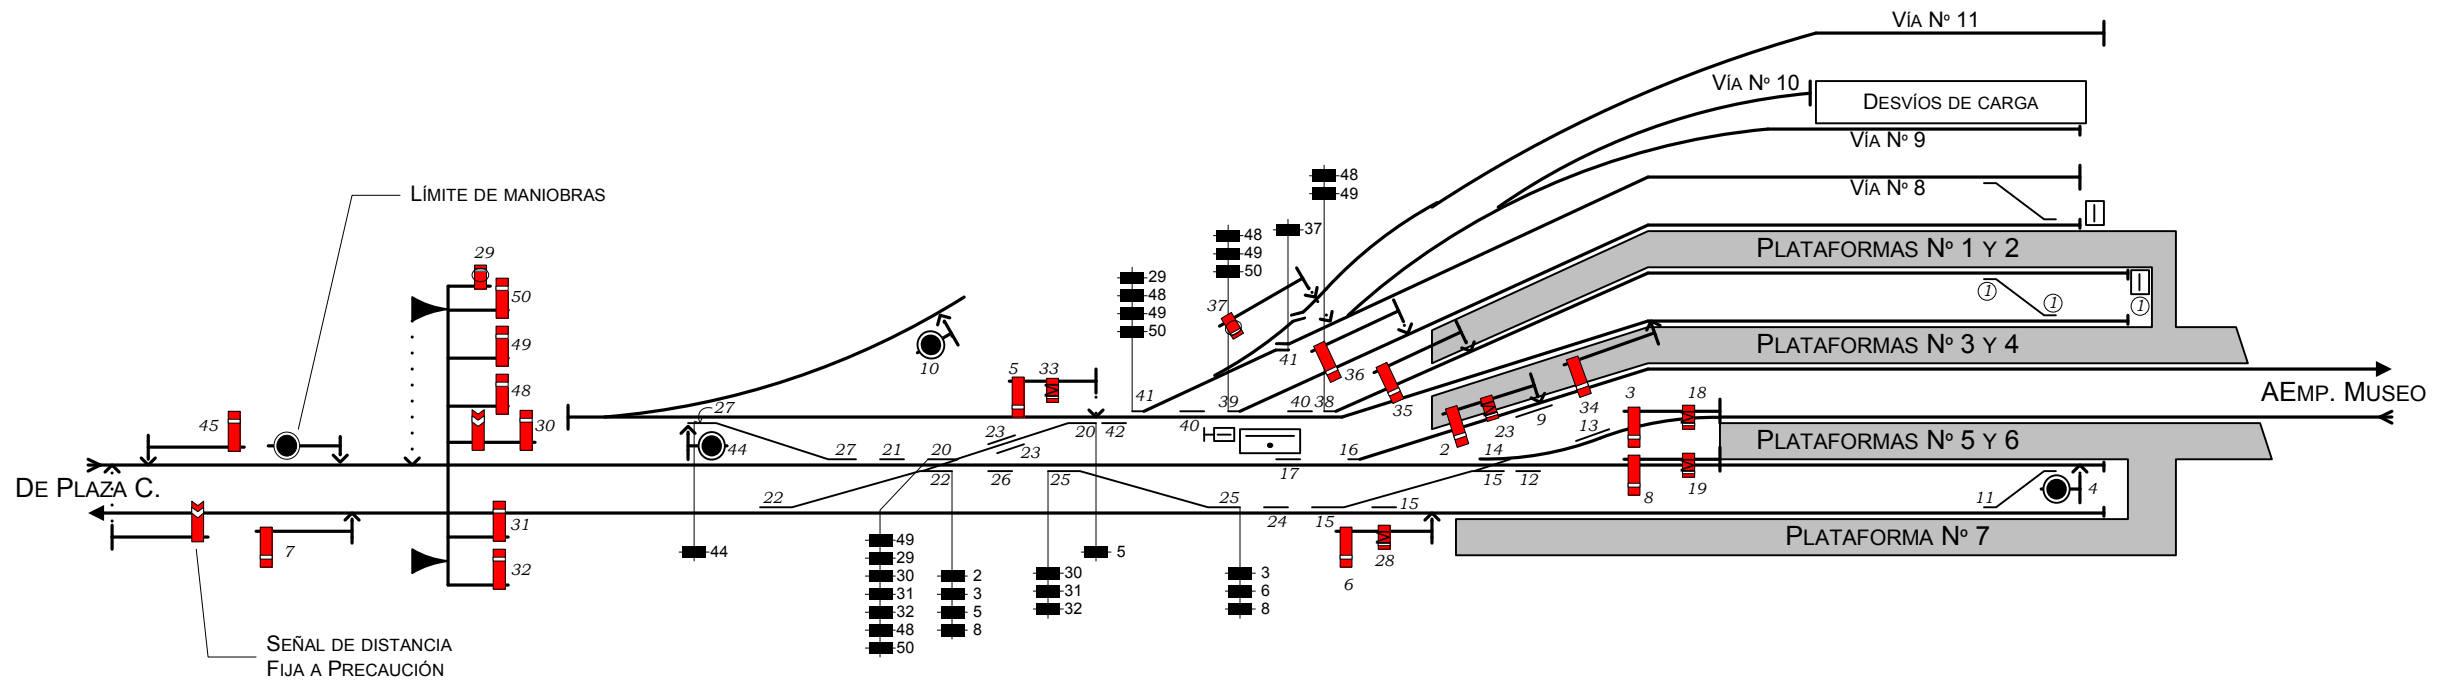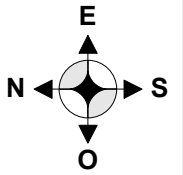

PALANCAS DE REPUESTO:

ESTACIÓN LA PLATA	
ESQUEMA DE CAMBIOS Y SEÑALES	28/02/2000
RICARDO A. AMODIO - AREA TRANSPORTE C.C.	5.15