


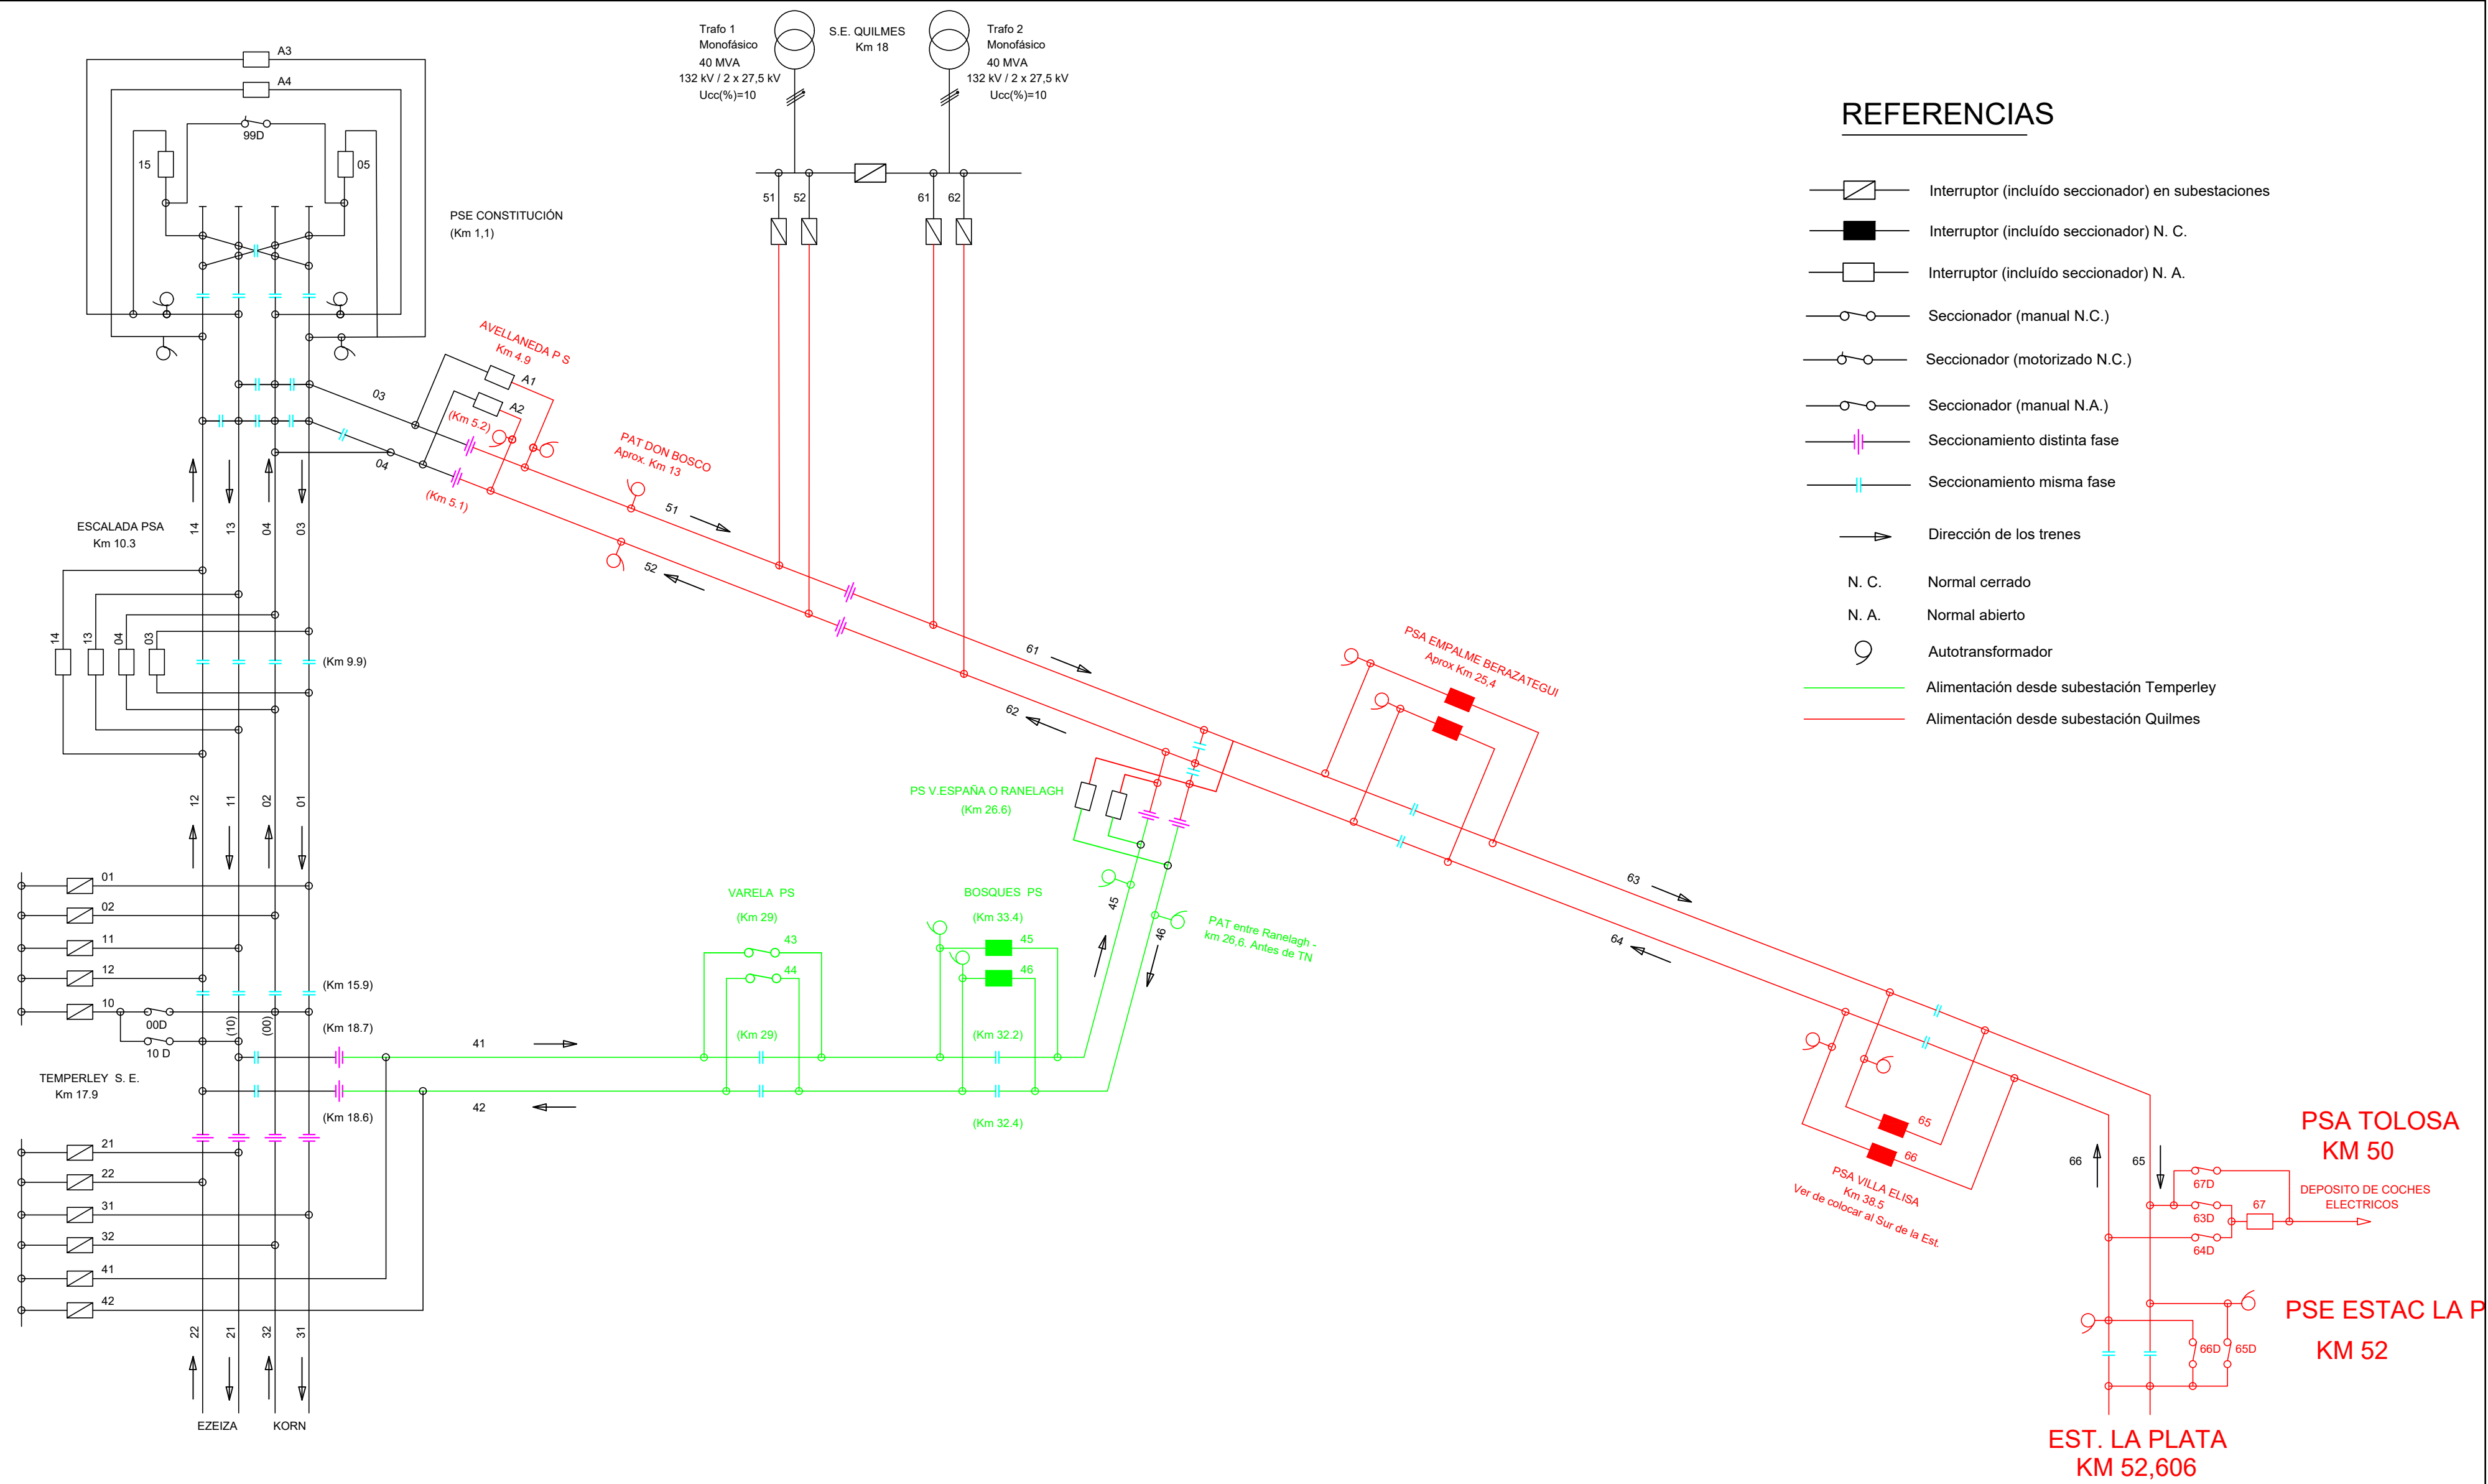

REFERENCIAS

- Interruptor (incluido seccionador) en subestaciones
- Interruptor (incluido seccionador) N. C.
- Interruptor (incluido seccionador) N. A.
- Seccionador (manual N.C.)
- Seccionador (motorizado N.C.)
- Seccionador (manual N.A.)
- Seccionamiento distinta fase
- Seccionamiento misma fase
- Dirección de los trenes
- N. C. Normal cerrado
- N. A. Normal abierto
- Autotransformador
- Alimentación desde subestación Temperley
- Alimentación desde subestación Quilmes

PLANO NO APTO PARA LA CONSTRUCCIÓN
PLANO ESQUEMÁTICO - SE ENTREGA A TÍTULO INFORMATIVO // ES RESPONSABILIDAD DEL OFERENTE / CONTRATISTA VERIFICAR LA CONCORDANCIA ENTRE LO INDICADO EN EL PLIEGO Y LOS PLANOS ADJUNTADOS.

LGR Línea Gral. Roca UGOFE S.A. GERENCIA OBRAS E INGENIERÍA	Obra: ---		UGOFE S.A.	
	Ubicación: KILO 18 III QUILMES R. AVELLANEDA - LA PLATA		Proyecto: ---	
	ESQUEMA GENERAL DE ALIMENTACIÓN DE CATENARIA / S.E. QUILMES		Diseño/Modificación: ---	
			Revisión: ---	
			Total de Hojas: 1	
Escala: ---	Fecha: ---	- - - - - E L B 0 3 9 0 0		