



RAMAL AV-LP

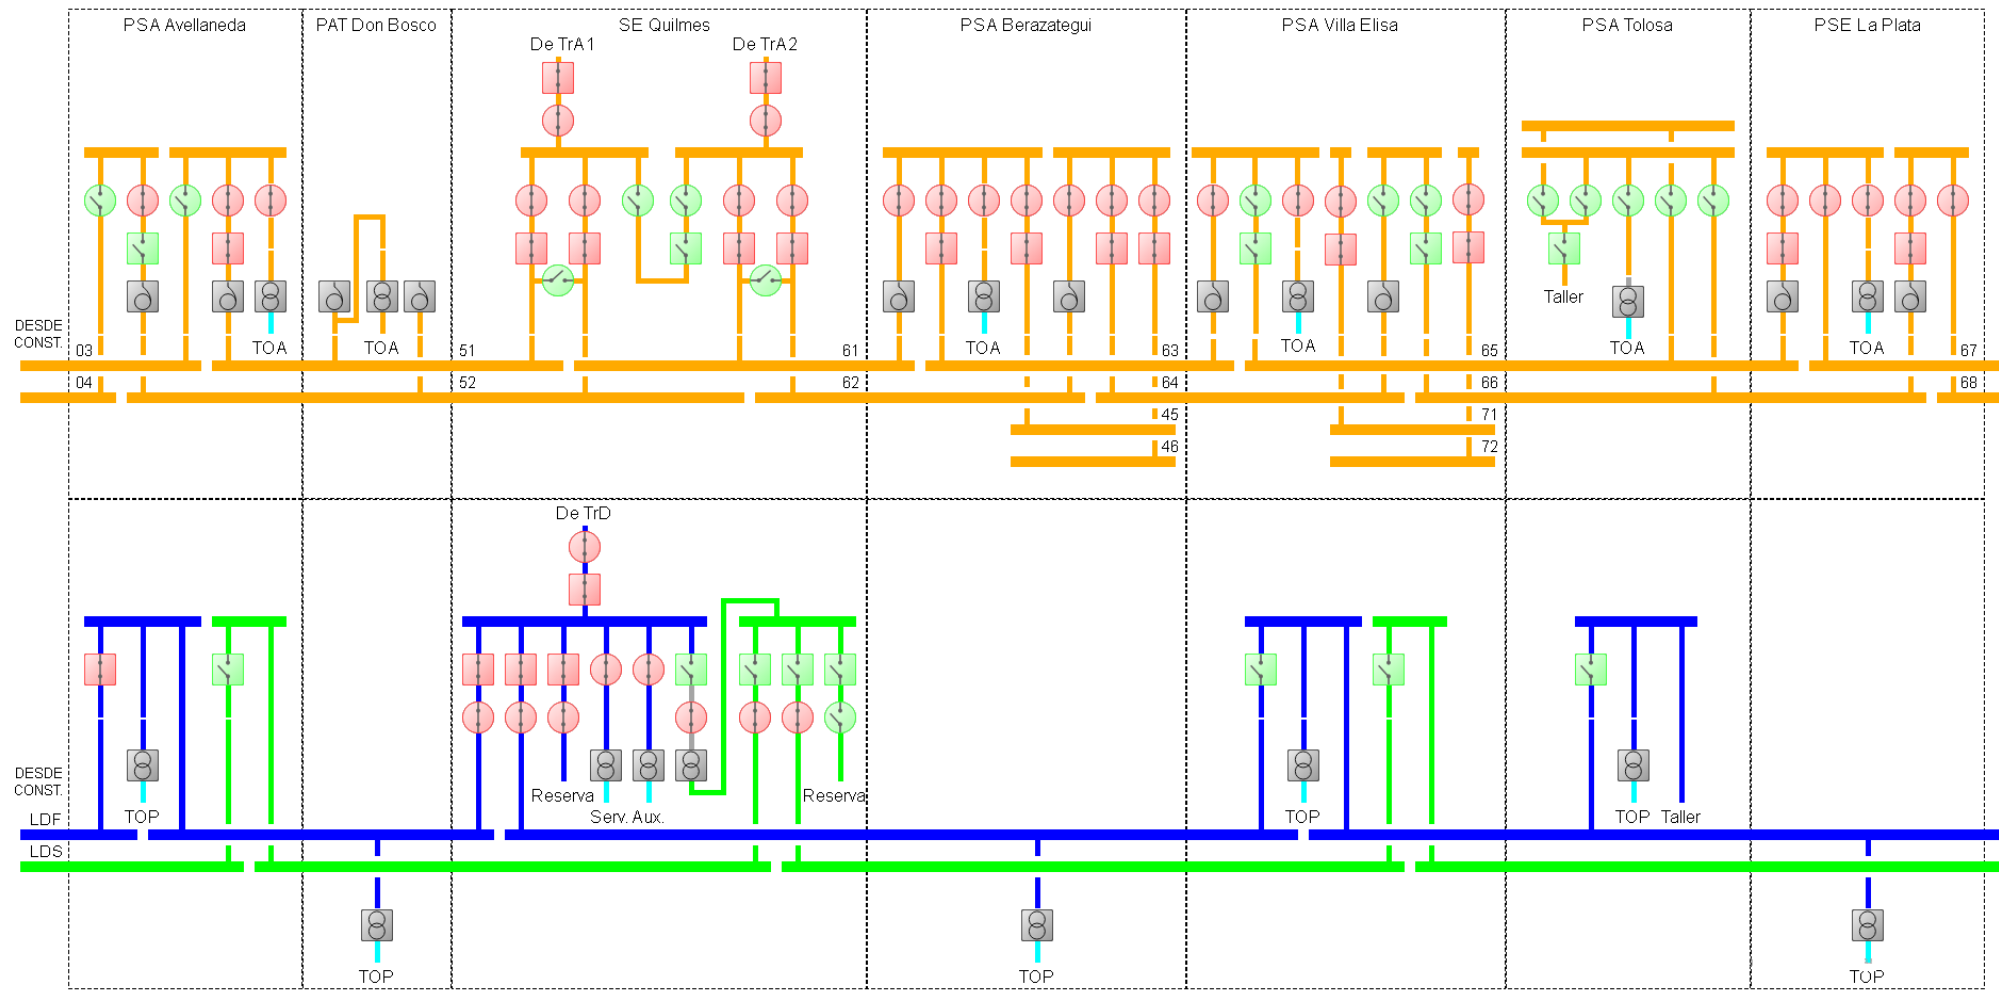


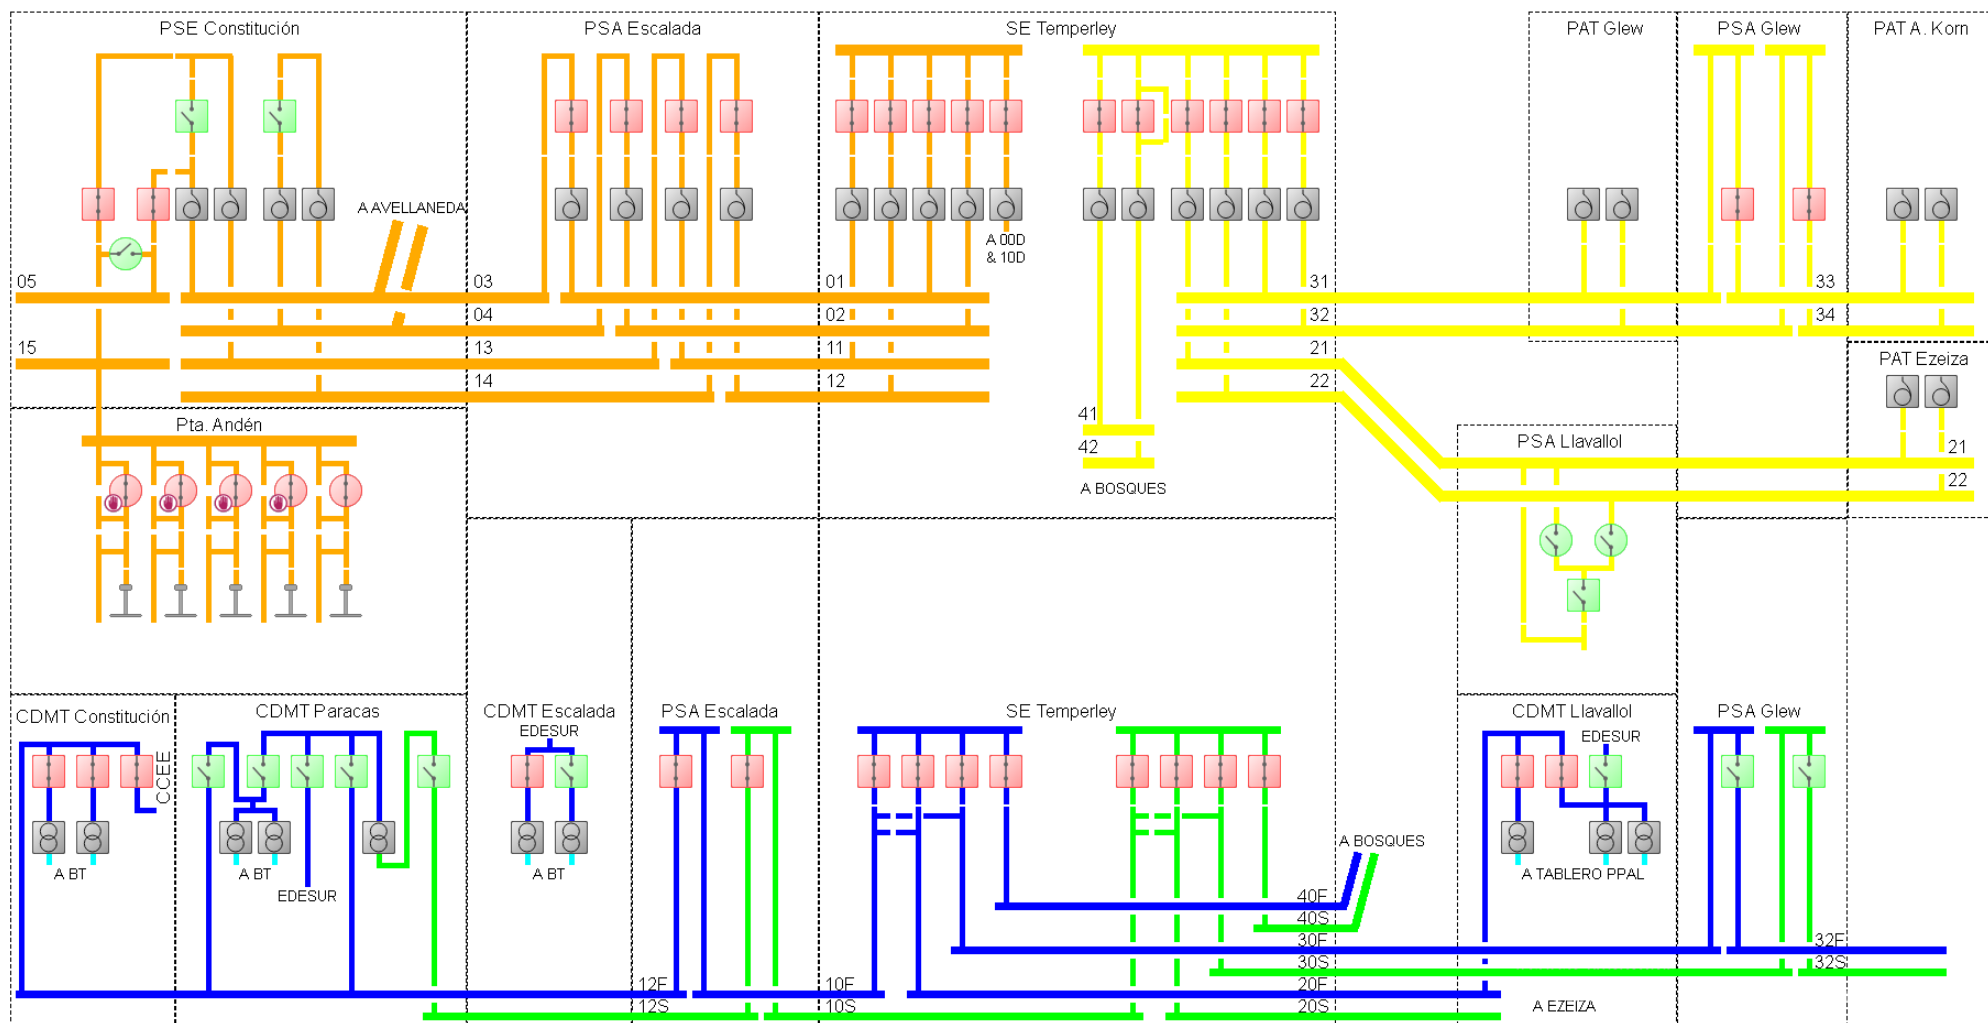

RAMAL CONST- KORN Y EZEIZA


SEQUI

UNIFILAR 132kV

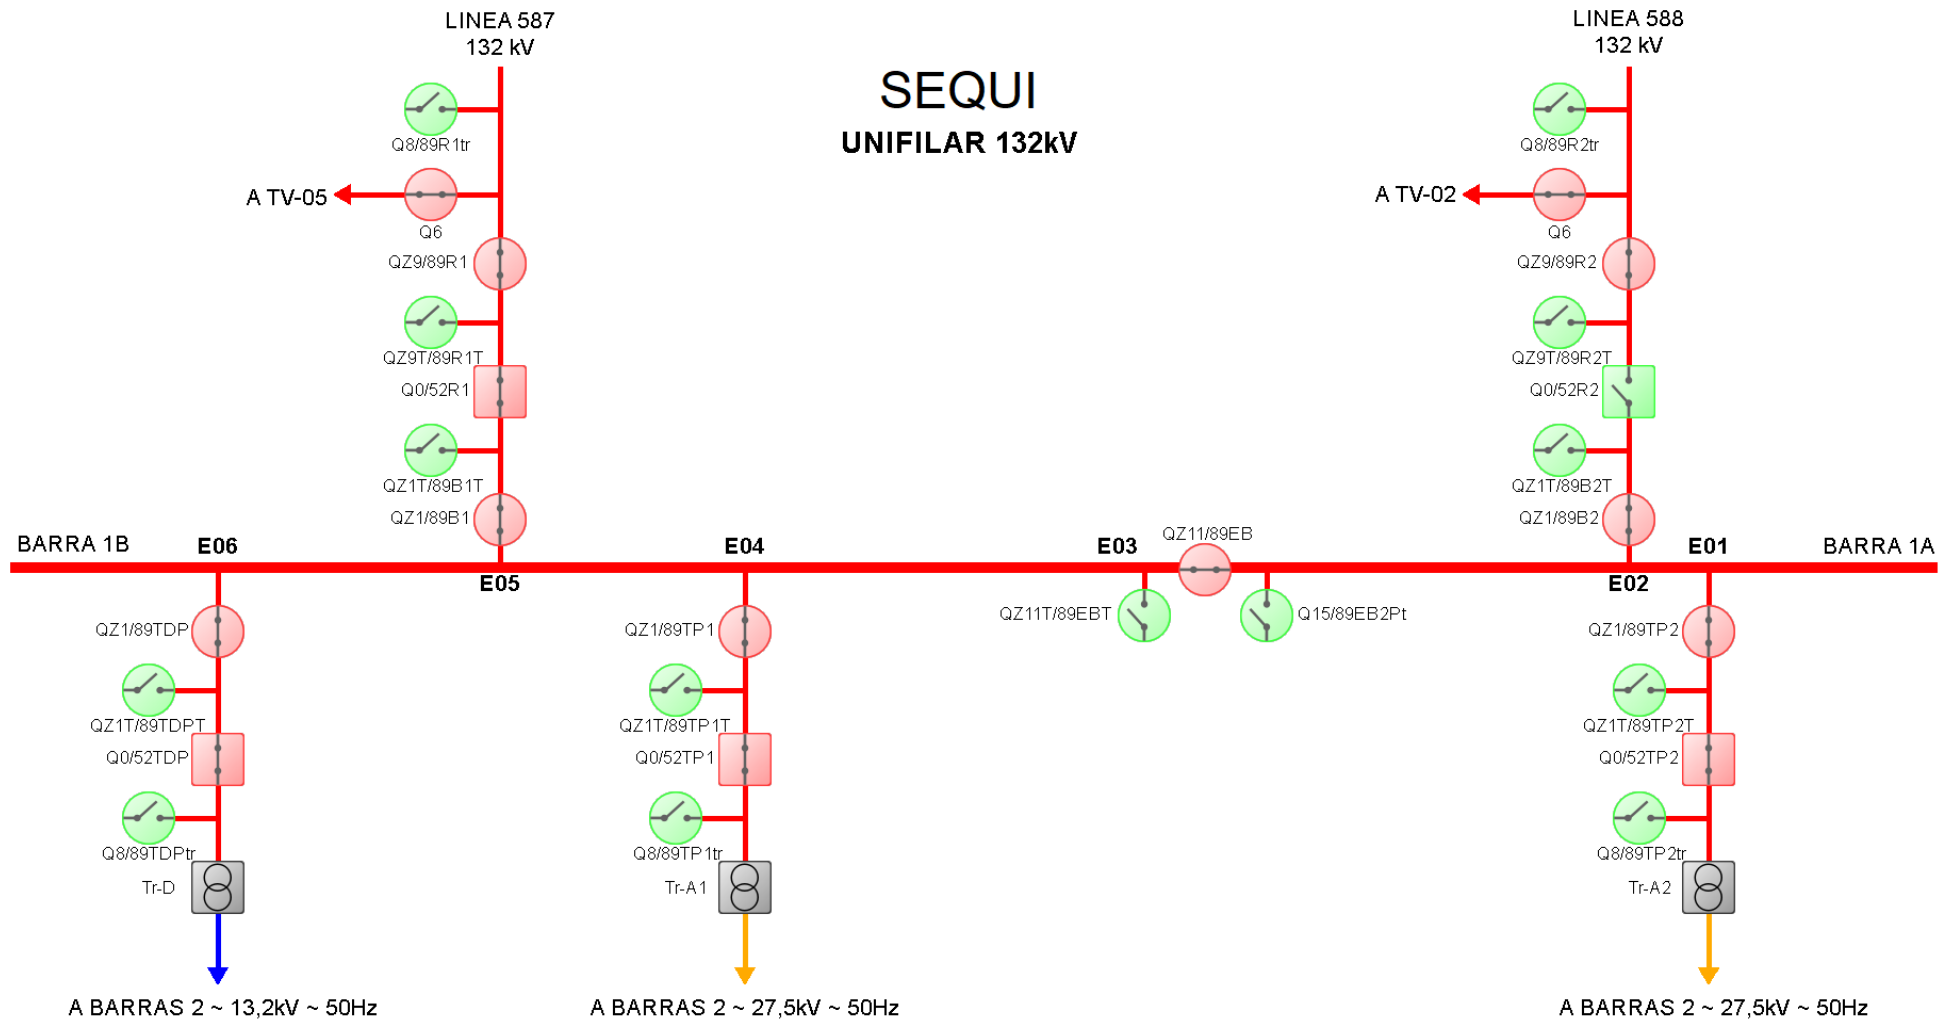


SEQUI

UNIFILAR 27,5kV

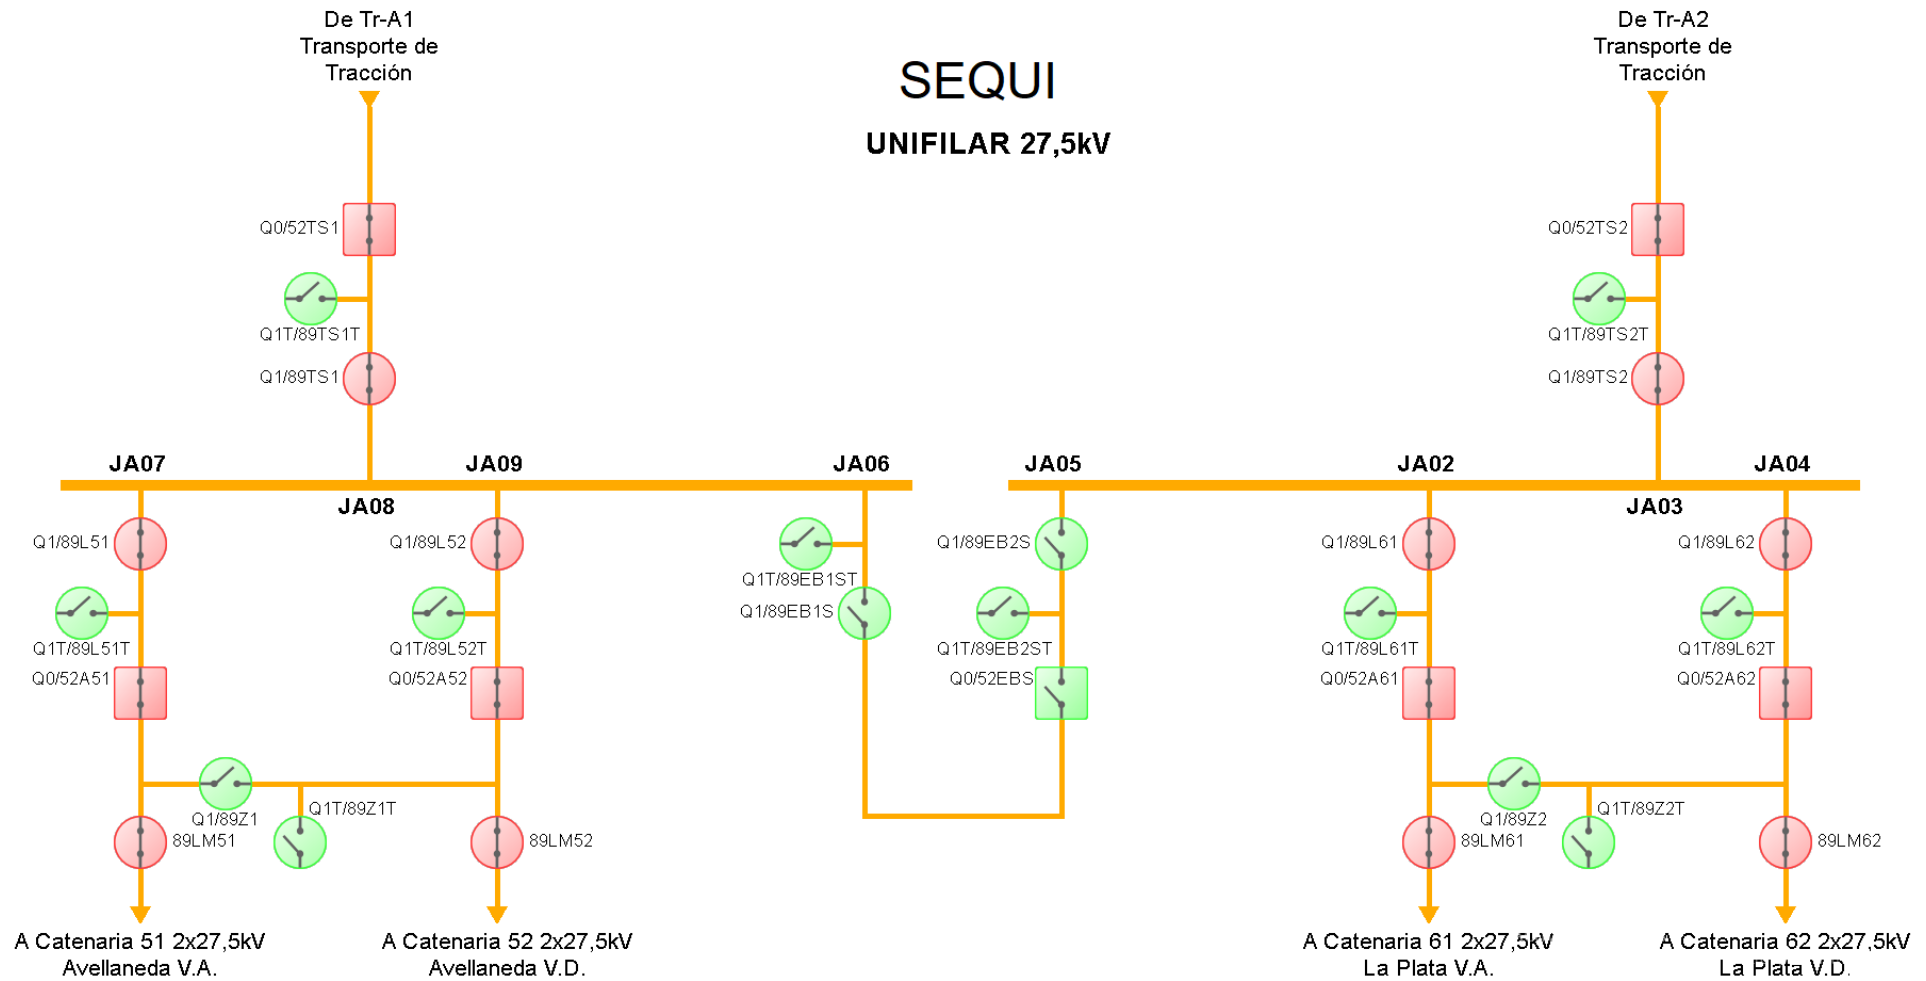



SEQUI

UNIFILAR 13,2kV

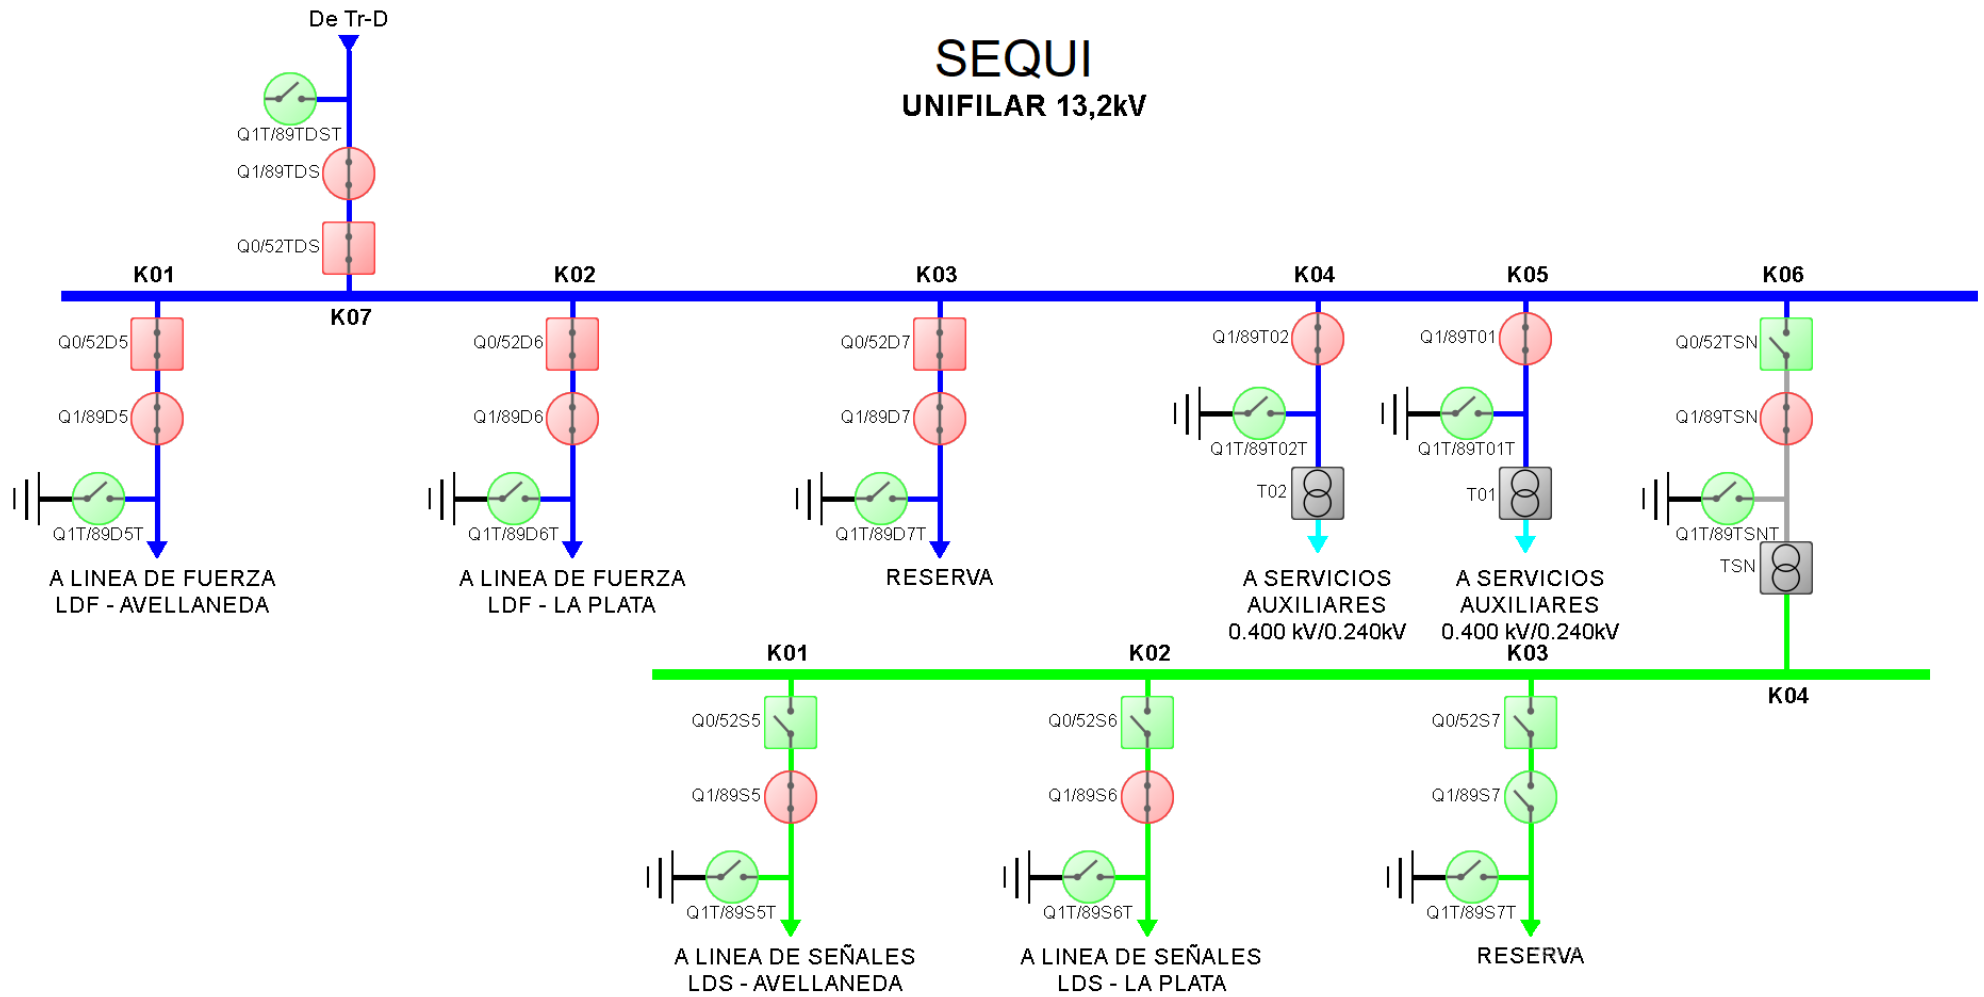


PSA AVELLANEDA


27,5 KV

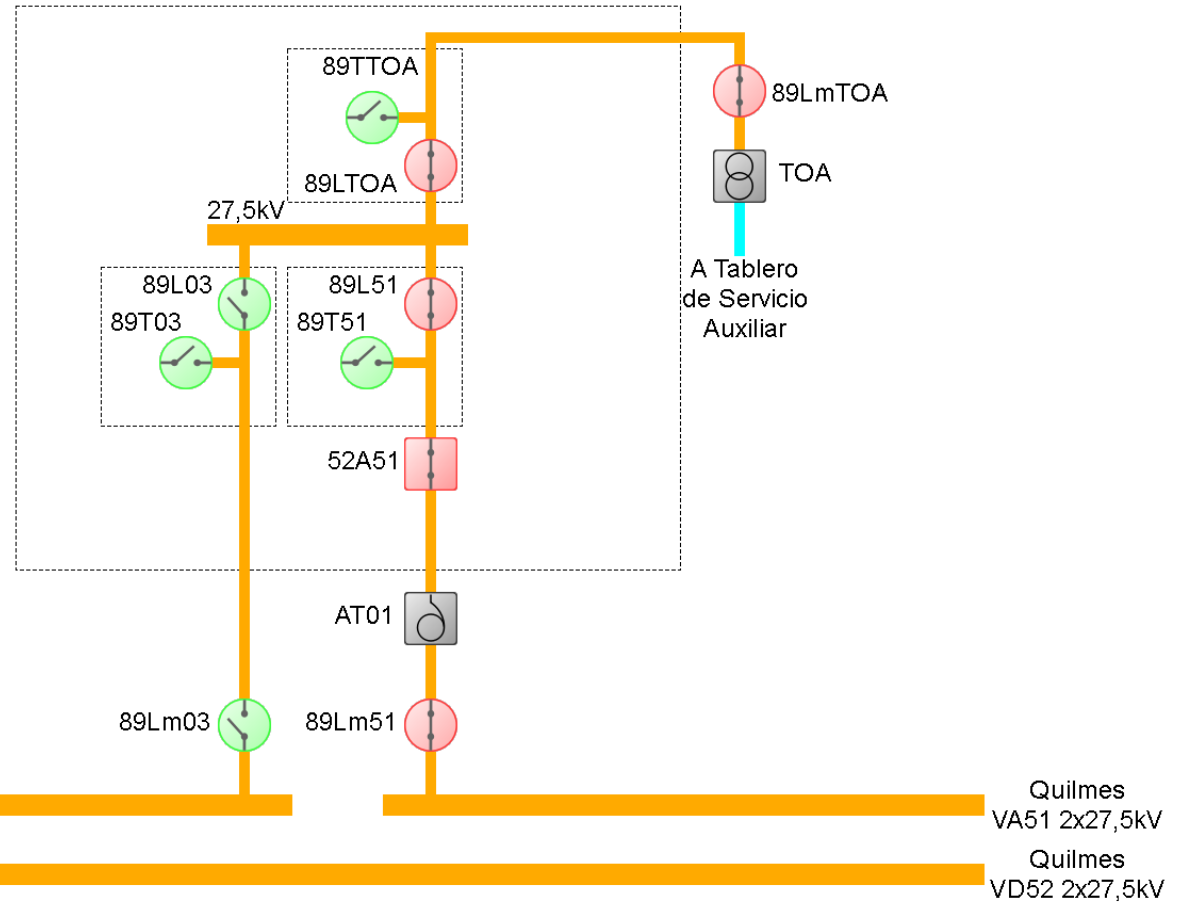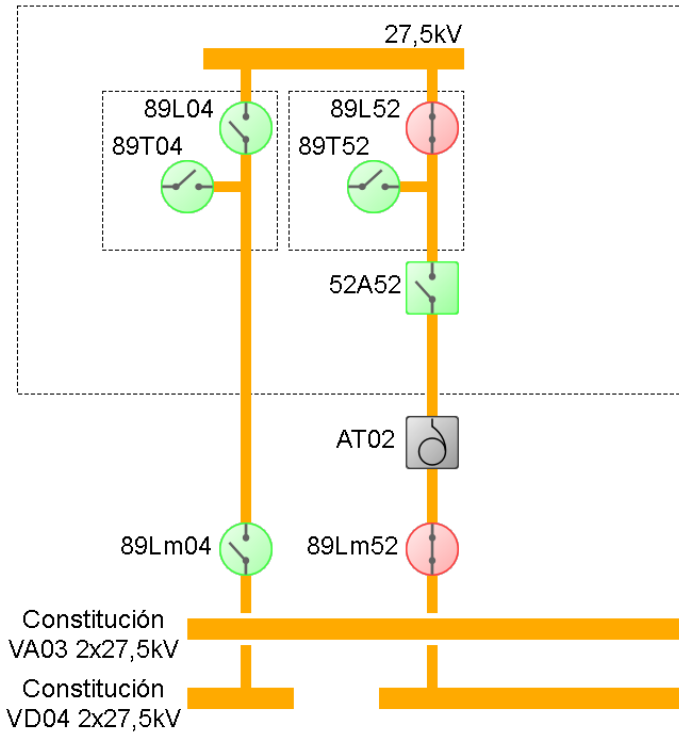


PSA AVELLANEDA
13,2 KV

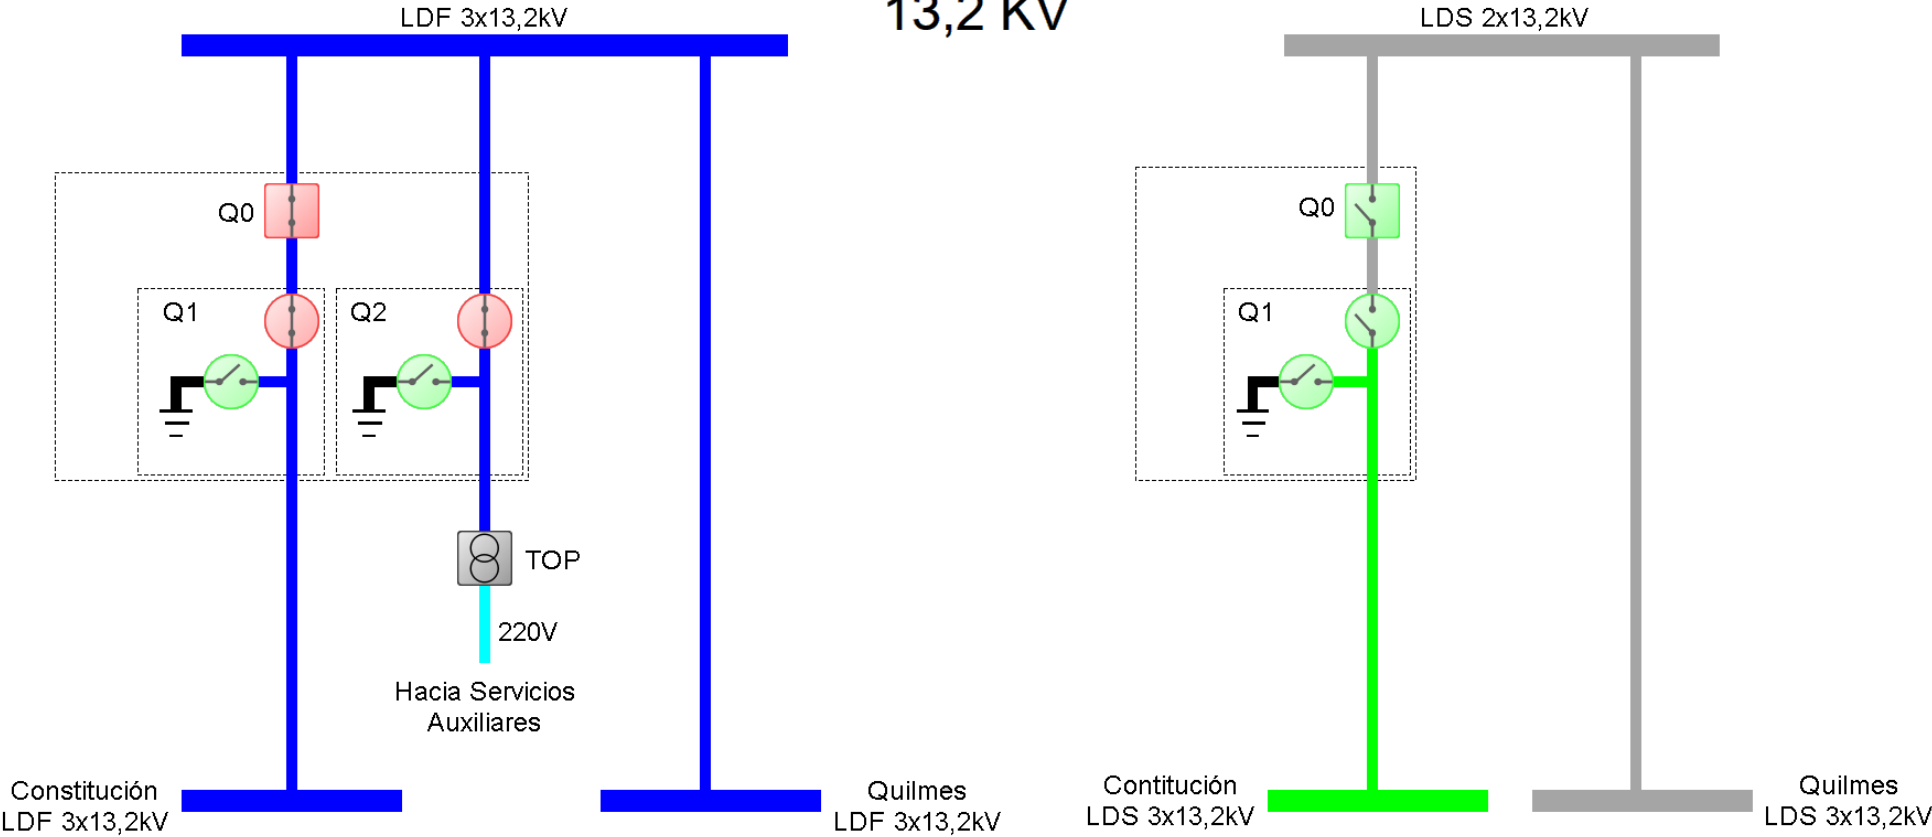


27,5 KV

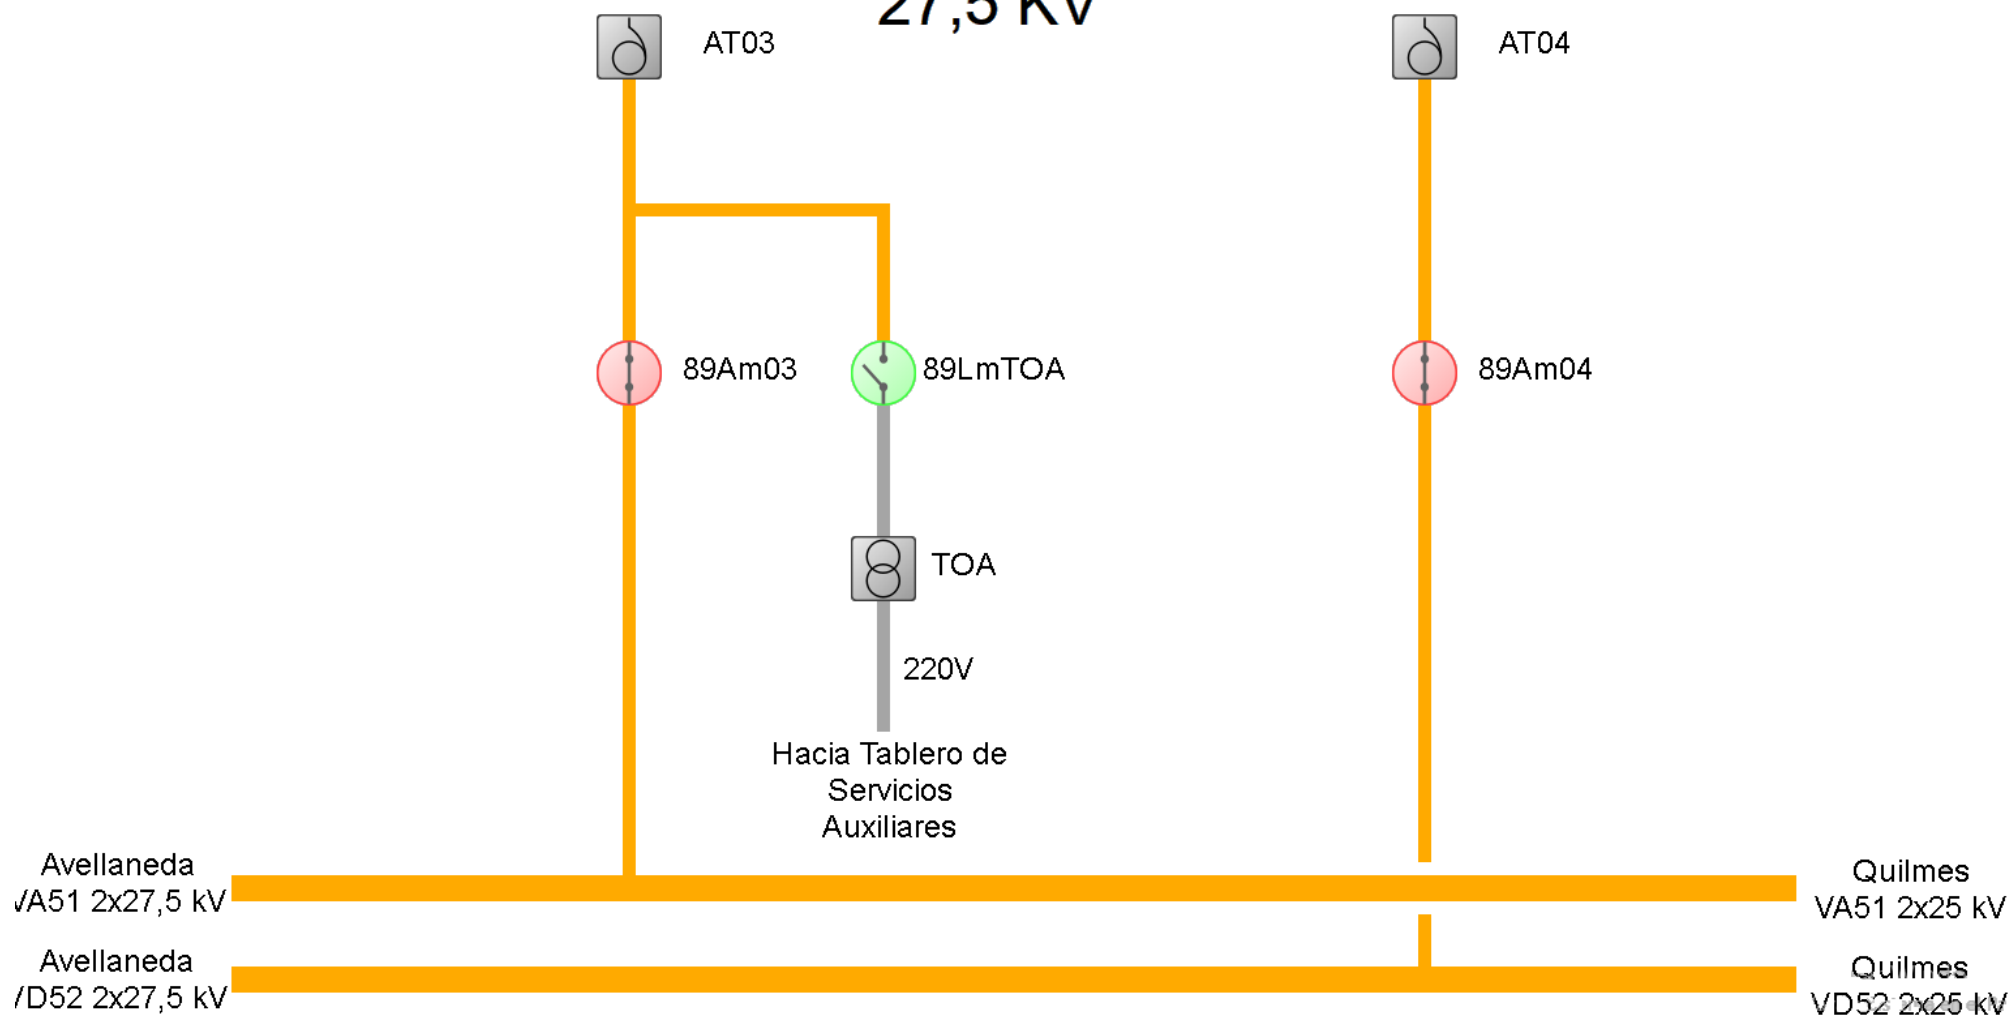


PSA BERAZATEGUI
27.5 KV

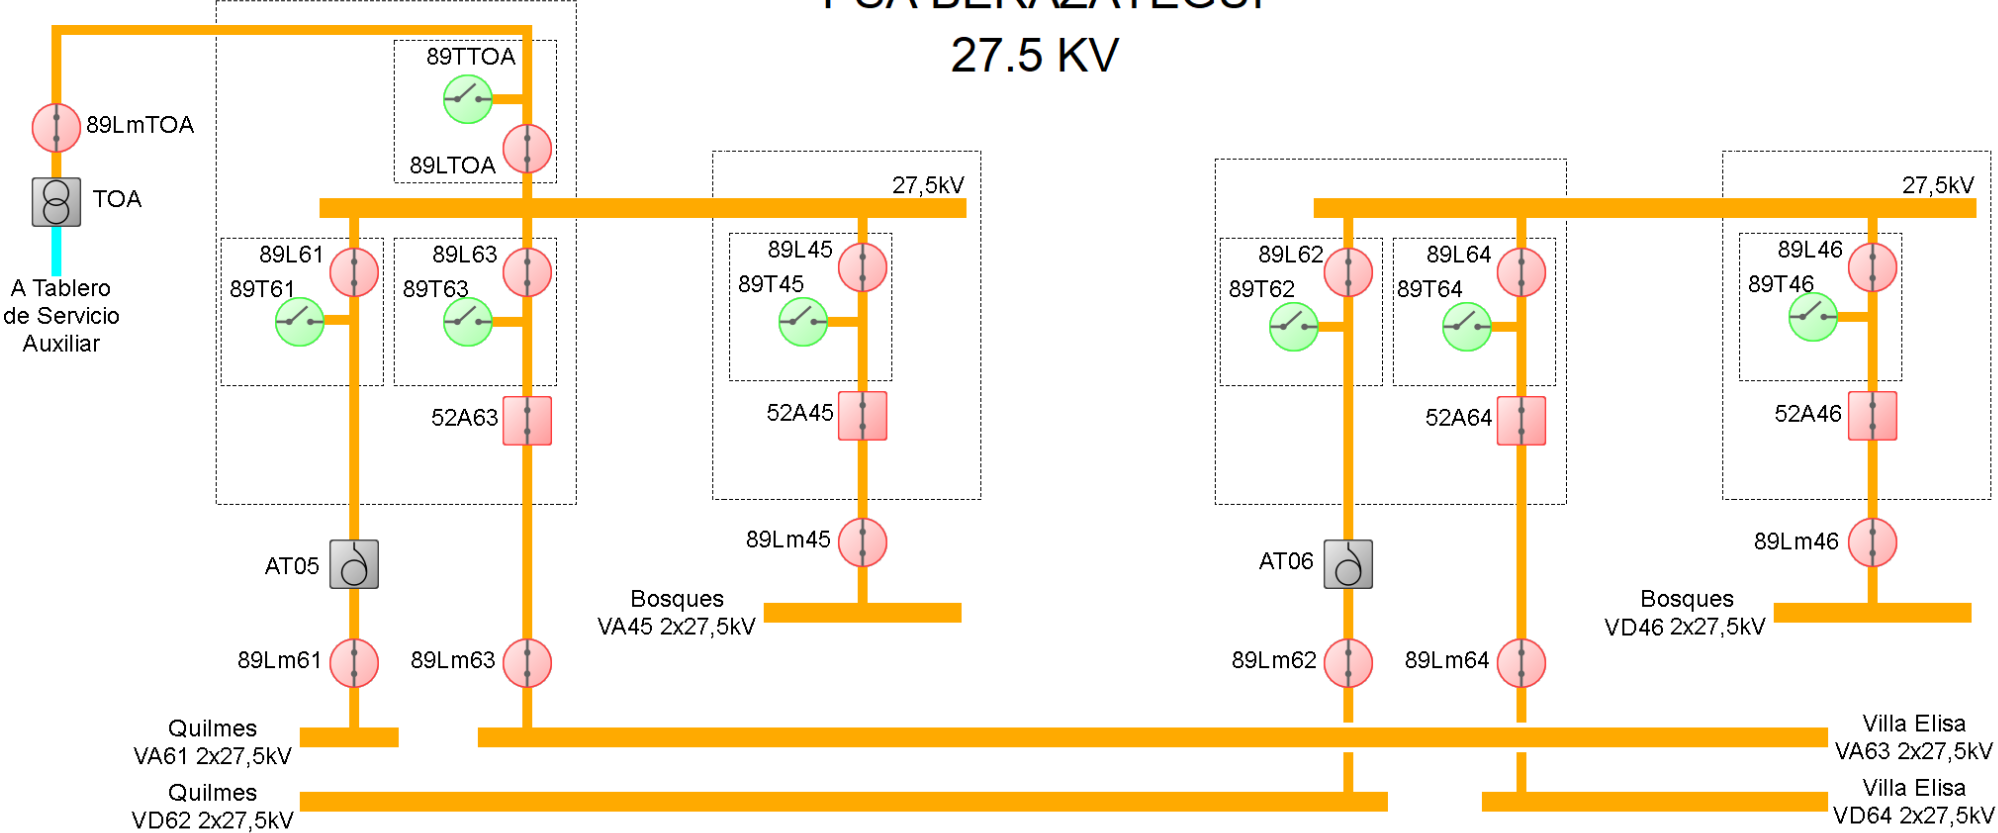


PSA VILLA ELISA 27.5 KV

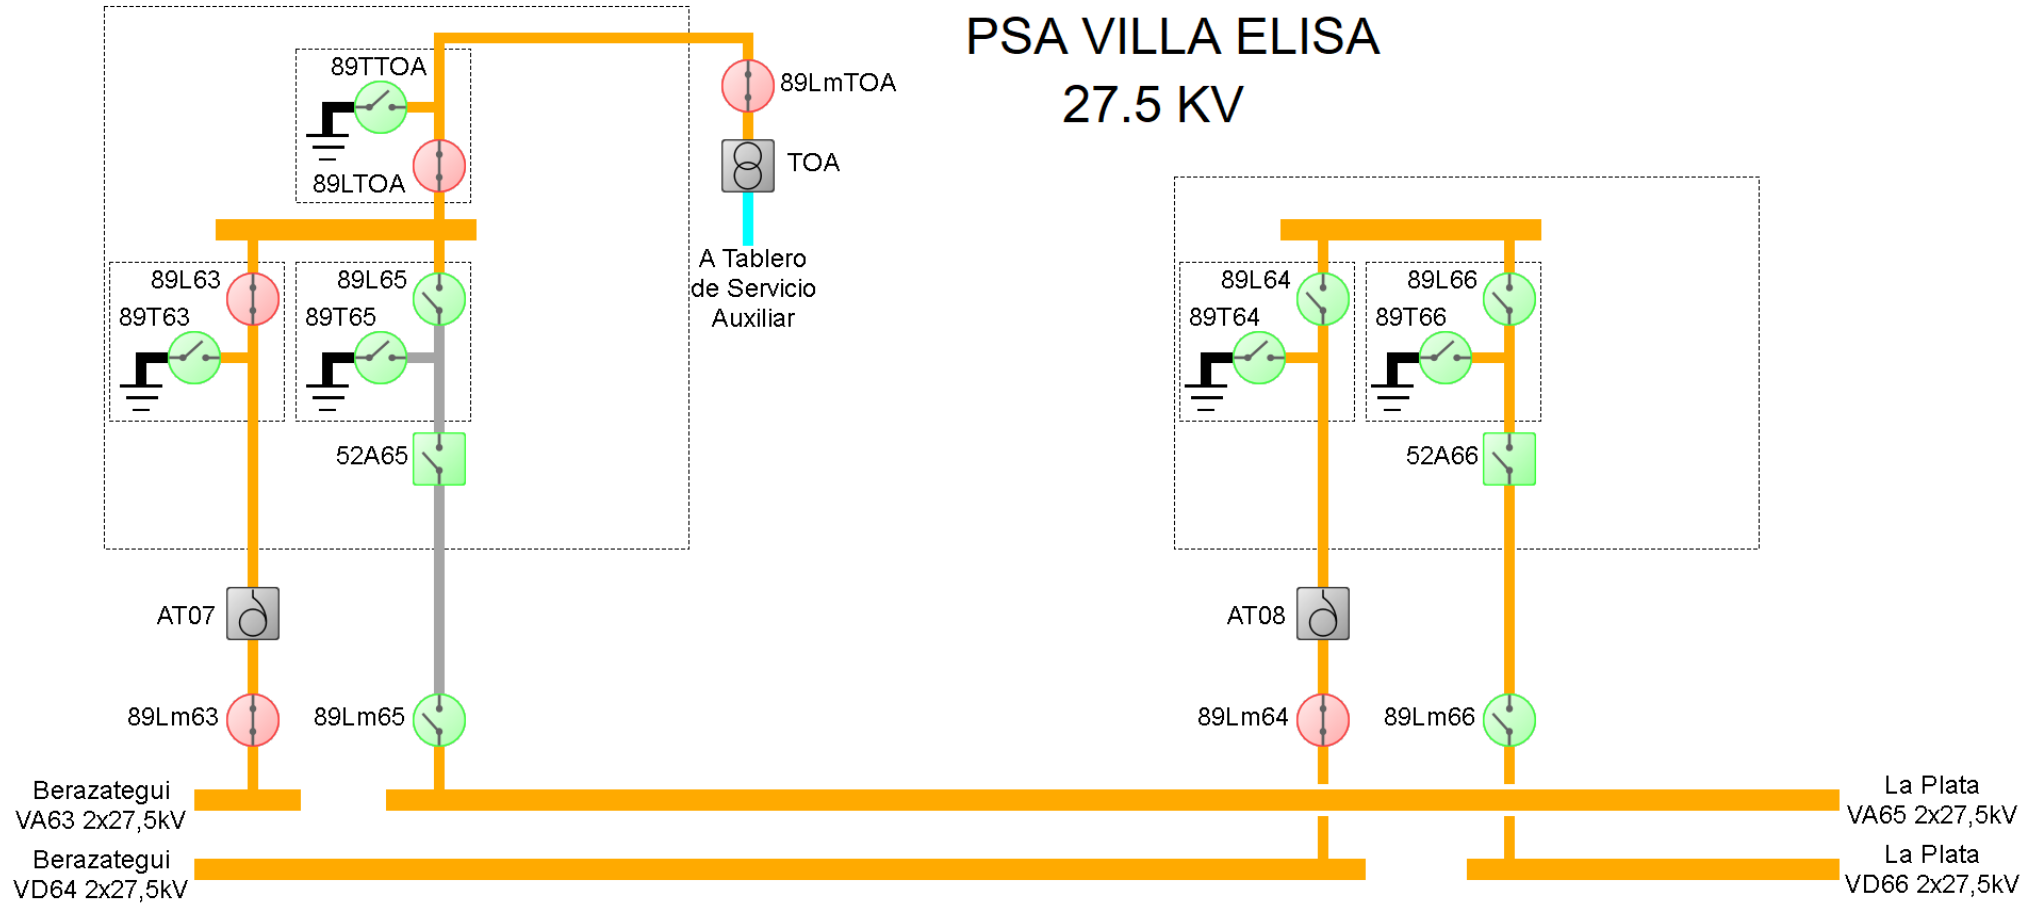

PSA VILLA ELISA
13.2 KV

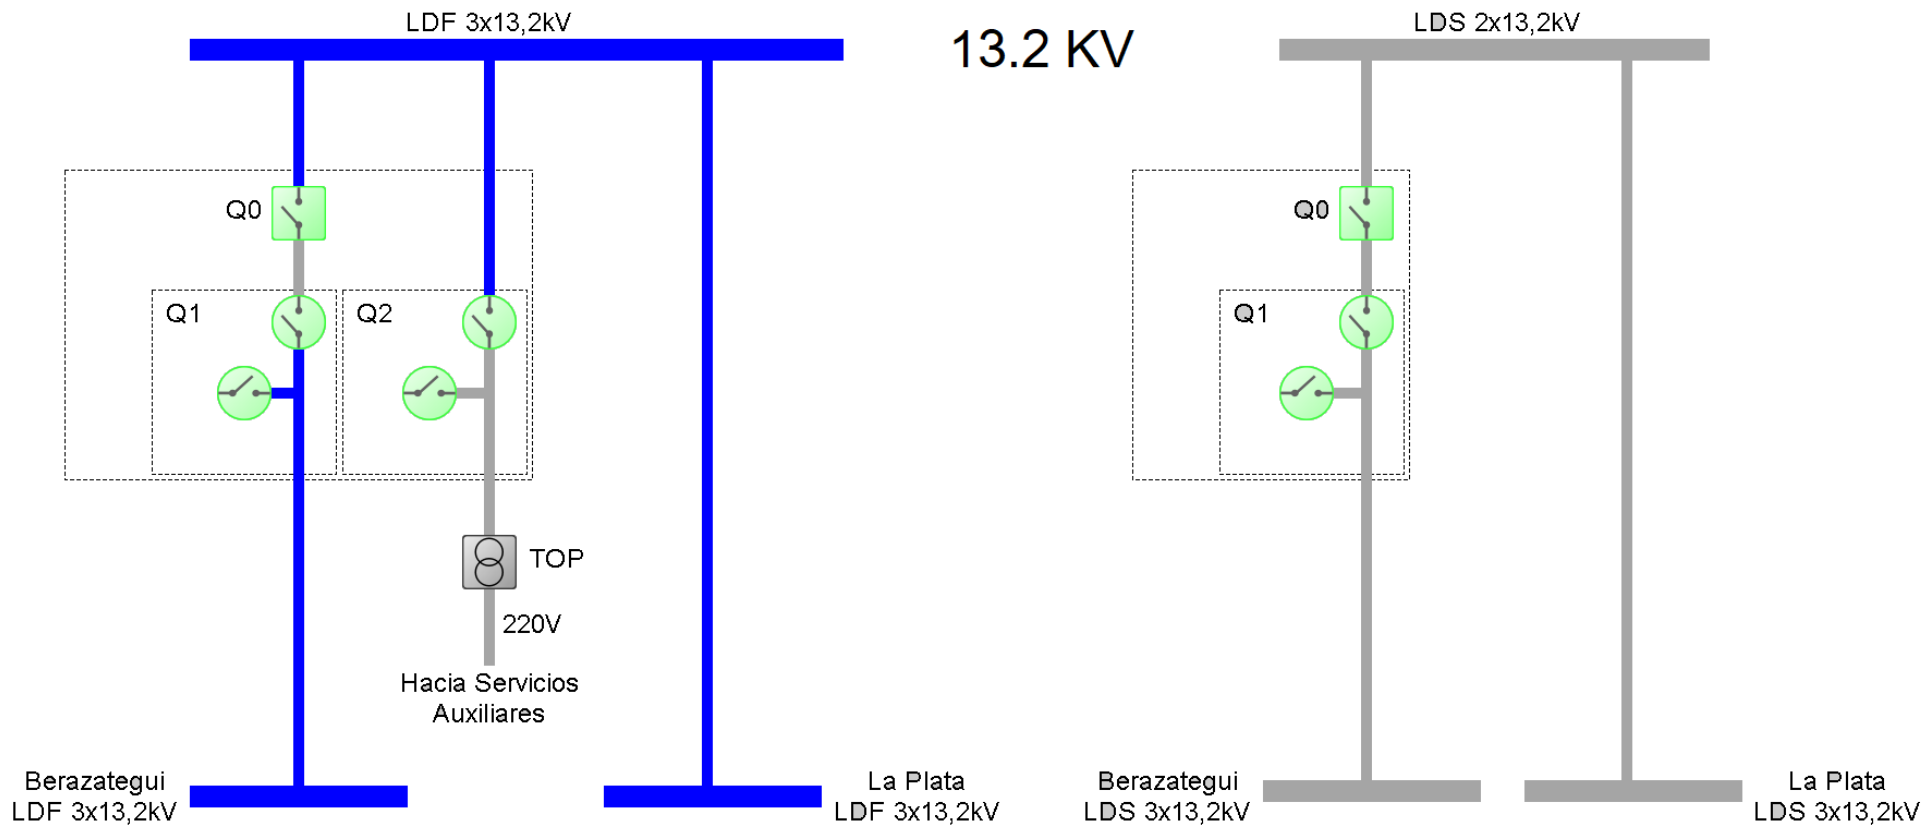

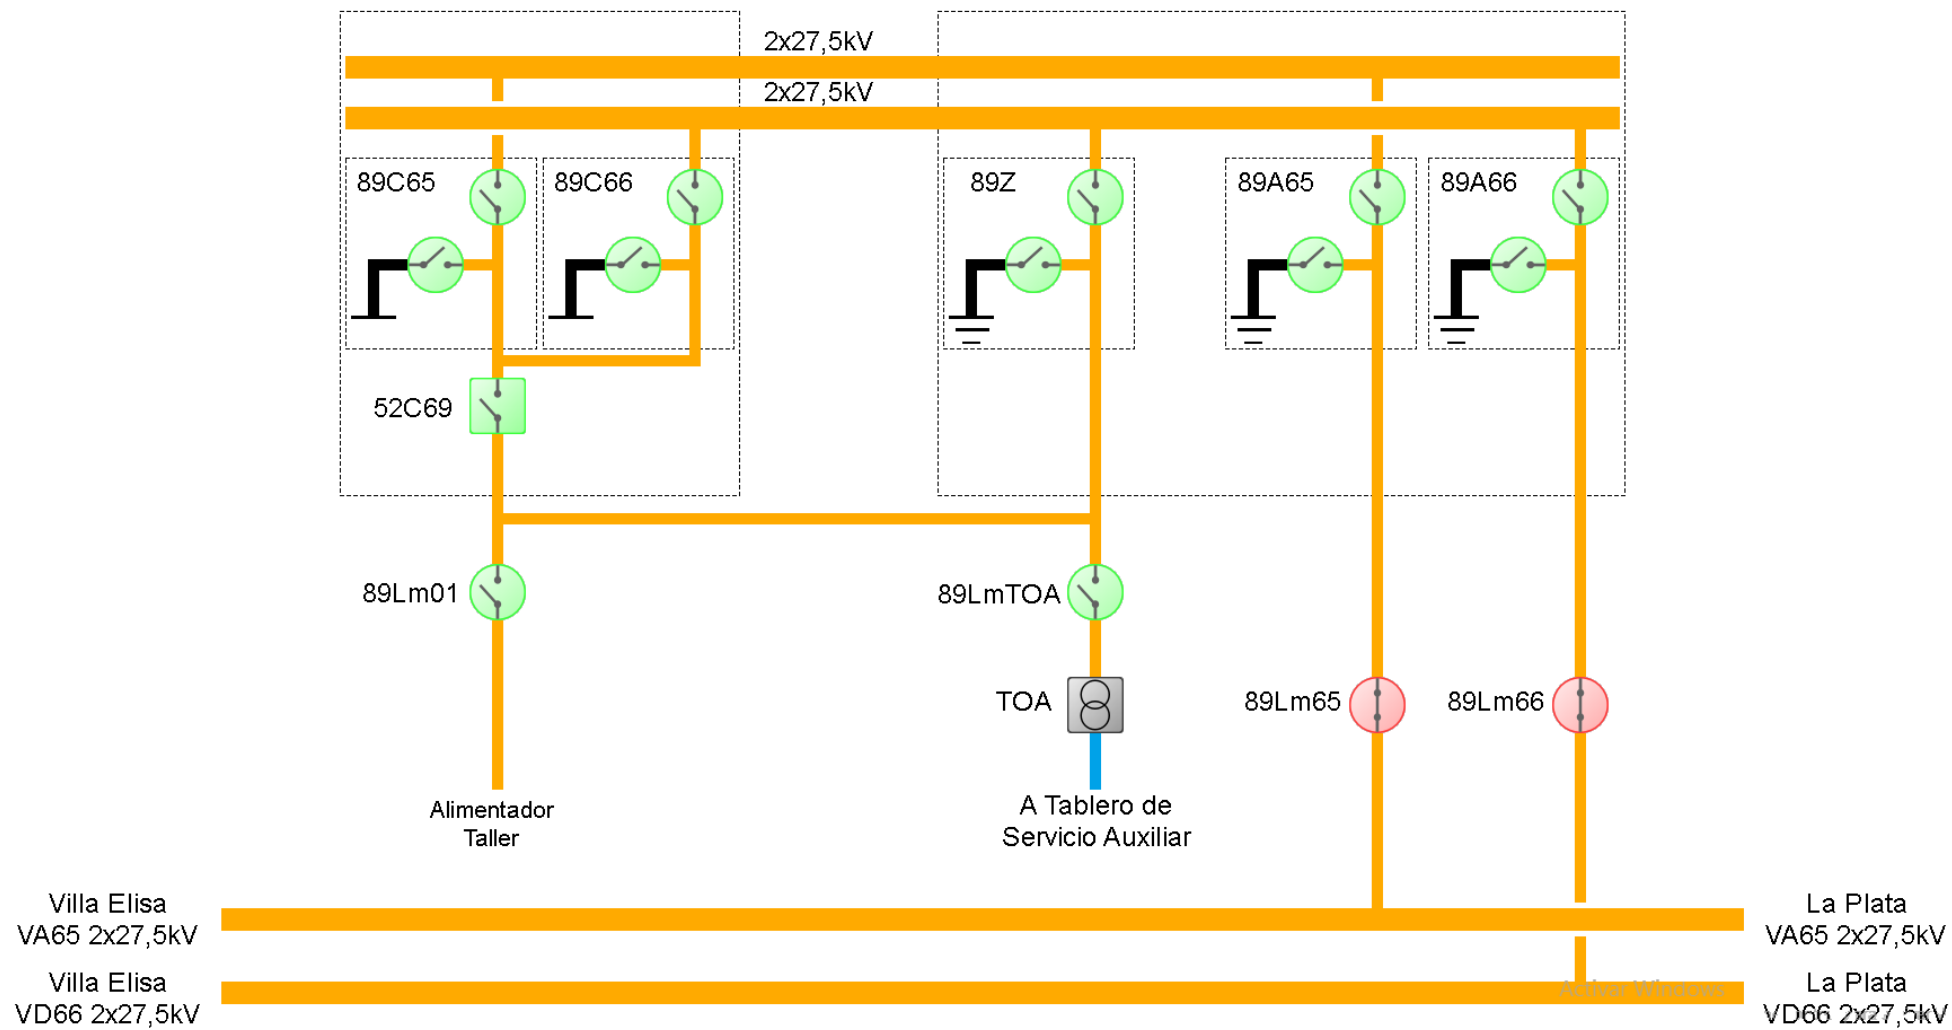


PS TOLOSA 27,5 KV

PS TOLOSA

13,2 KV

LDF
3x13,2kV

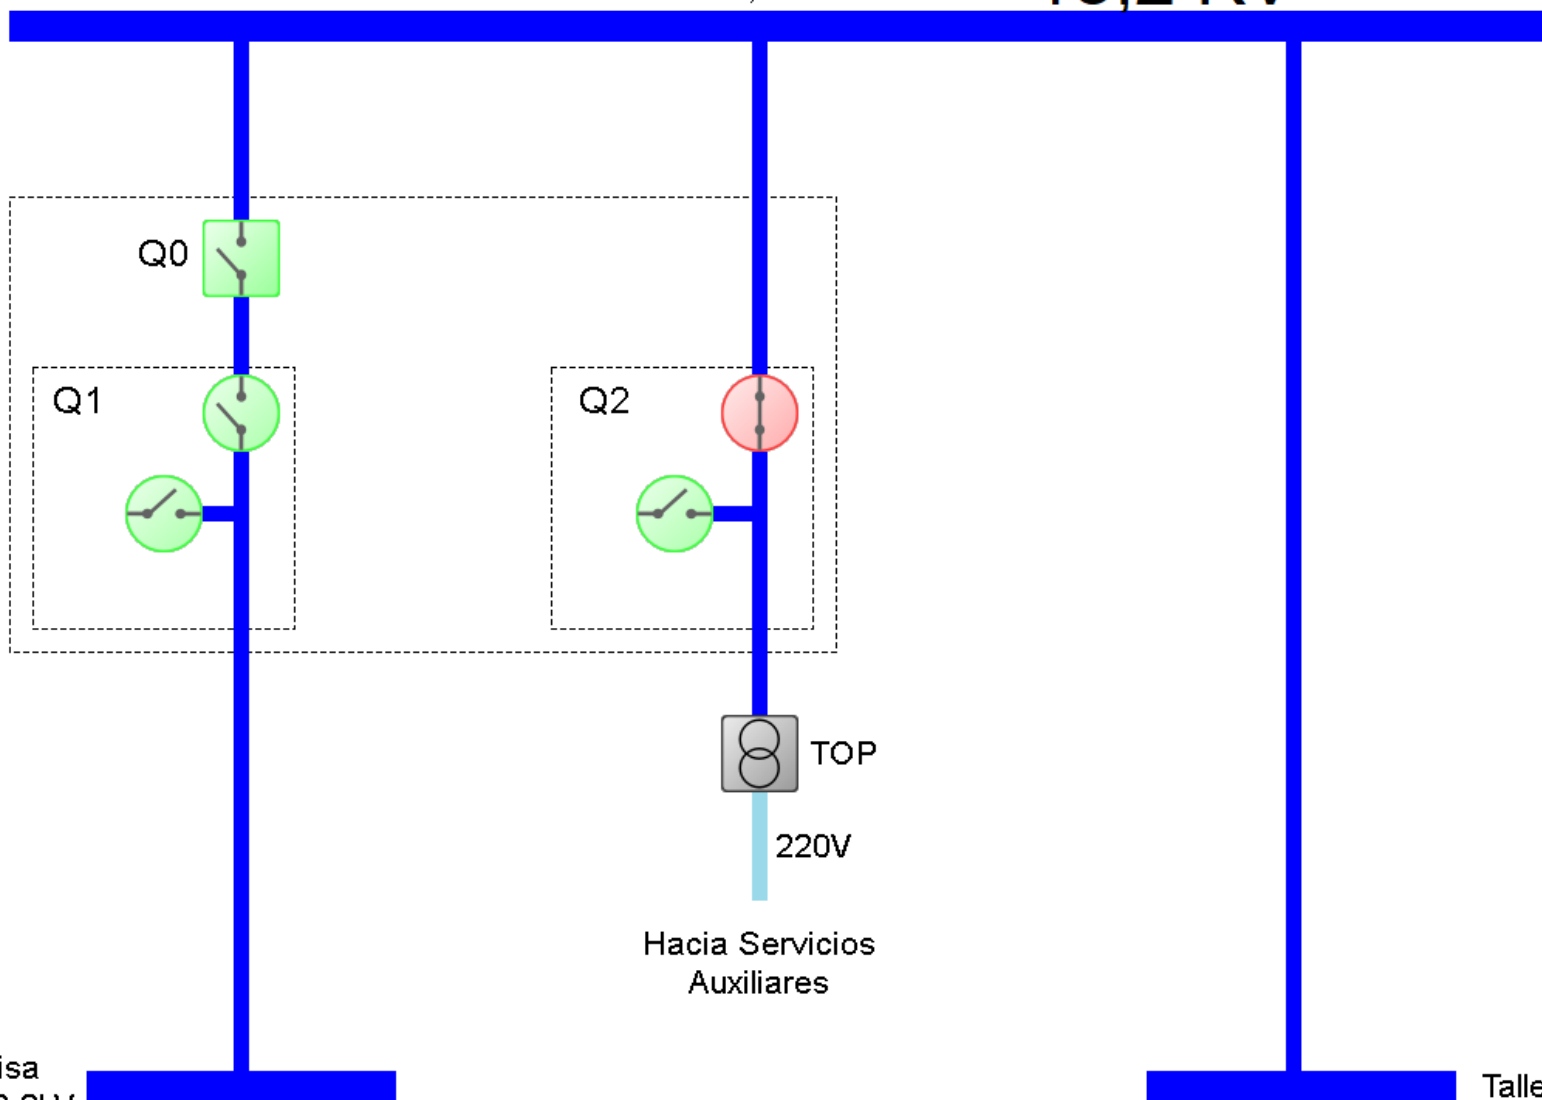

Villa Elisa
LDF 3x13,2kV

Taller Tolosa

PSE LA PLATA 27,5 KV R

